


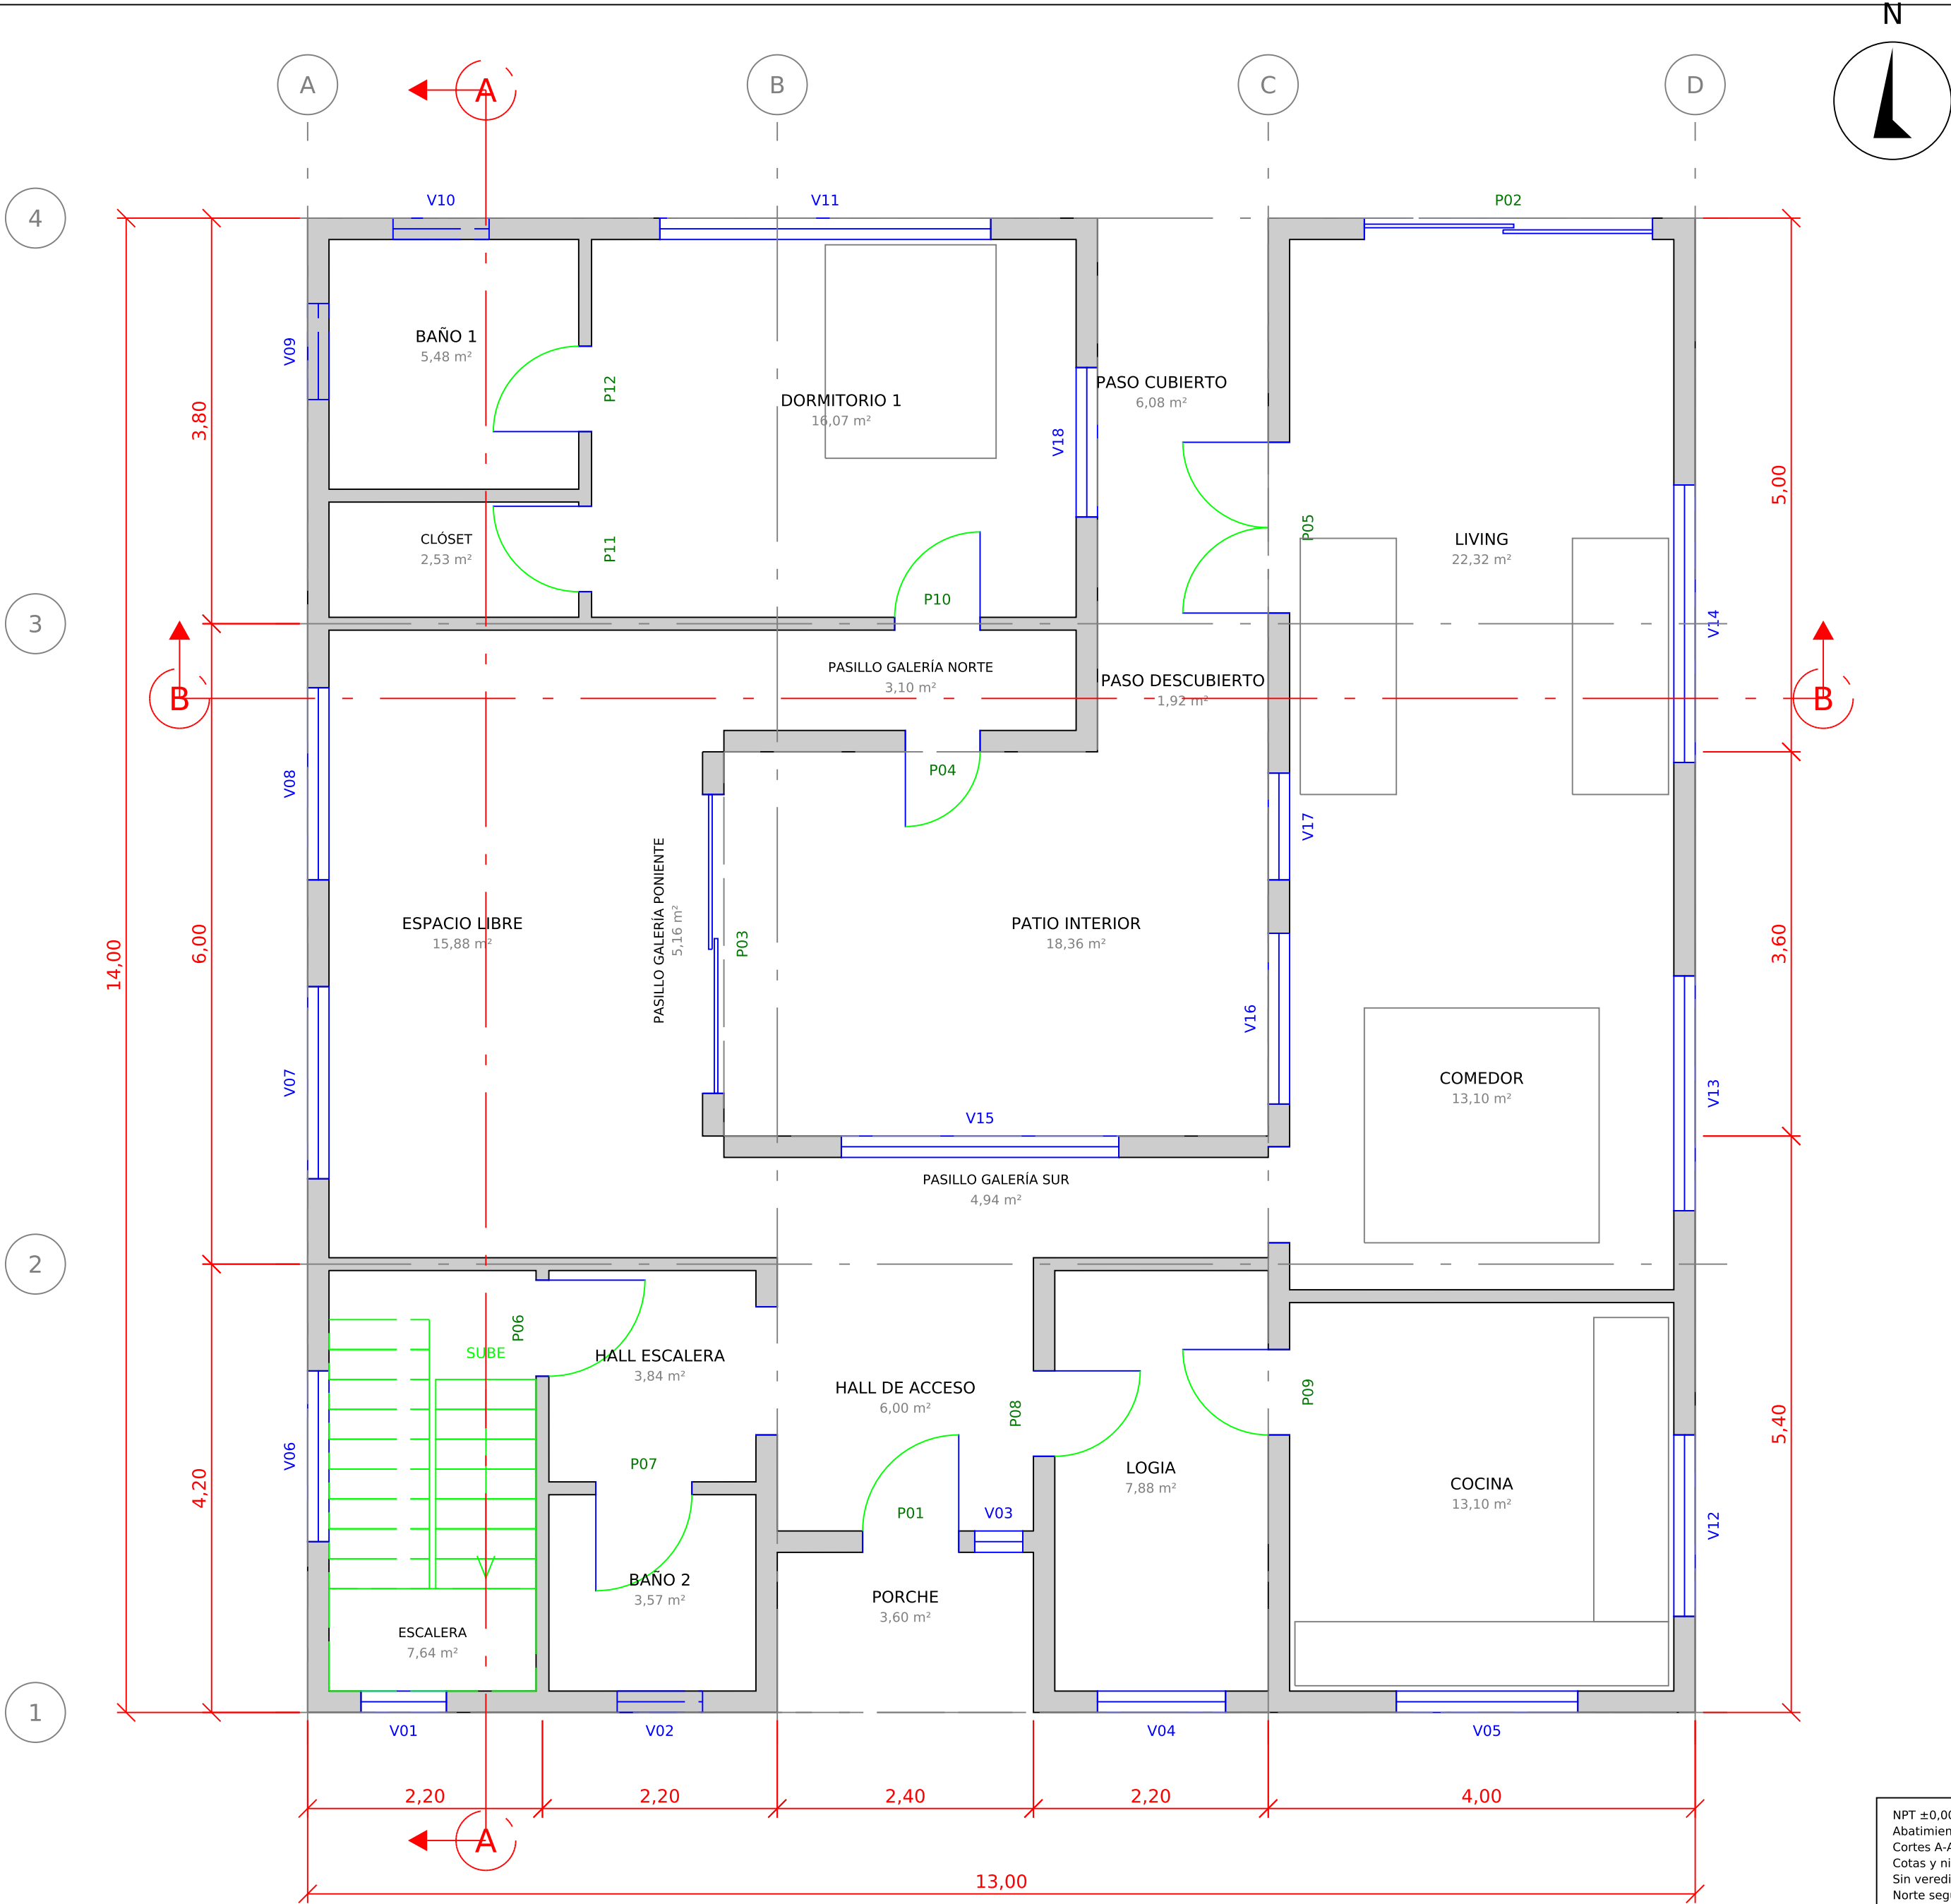

PLANTA PRIMER PISO

1:50

CUADRO DE SUPERFICIES — Primer Piso

Recinto	A ejes (doc)	Útil (modelo)
Escalera	9,24	7,64
Baño 2	4,62	3,57
Hall Escalera	4,62	3,84
Hall de Acceso	6,48	6,00
Logia	9,24	7,88
Porche (ext.)	3,60	3,60
Espacio Libre	17,40	15,88
Pasillo Galería Poniente	6,00	5,16
Pasillo Galería Sur	6,12	4,94
Pasillo Galería Norte	4,20	3,10
Clóset	3,12	2,53
Baño 1	6,76	5,48
Dormitorio 1	18,24	16,07
Cocina	15,60	13,10
Comedor	14,80	13,10
Living	25,60	22,32
Patio Interior (ext.)	18,36	18,36
Paso Cubierto (ext.)	6,08	6,08
Paso Descubierta (ext.)	1,92	1,92
Suma recintos interiores	152,04	130,61

A ejes: coincide con el cuadro del documento rev. G (verificado recinto por recinto).
Útil: superficie medida del Space del modelo FreeCAD, descontada la huella de muros.
Exteriores (porche, patios, paso) no suman.

CUADRO DE VANOS

Cód.	Tipo	Ancho x alto	Antepecho	Dintel	Apertura (patrón de diseño)
P01	Puerta	0,90 x 2,10	-0,00	2,10	abre a Hall de Acceso, bisagra der.
P02	Puerta	2,70 x 2,36	-0,00	2,36	corredera
P03	Puerta	2,80 x 2,35	-0,00	2,35	corredera
P04	Puerta	0,70 x 2,10	-0,00	2,10	abre a Patio Interior, bisagra der.
P05	Puerta	1,60 x 2,35	-0,00	2,35	2 hojas a Paso Cubierto, bisagra ambos
P06	Puerta	0,90 x 2,10	-0,00	2,10	abre a Hall Escalera, bisagra izq.
P07	Puerta	0,90 x 2,10	-0,00	2,10	abre a Baño 2, bisagra der.
P08	Puerta	0,80 x 2,10	-0,00	2,10	abre a Logia, bisagra izq.
P09	Puerta	0,80 x 2,10	-0,00	2,10	abre a Logia, bisagra der.
P10	Puerta	0,80 x 2,10	-0,00	2,10	abre a Dormitorio 1, bisagra der.
P11	Puerta	0,80 x 2,10	-0,00	2,10	abre a Clóset, bisagra der.
P12	Puerta	0,80 x 2,10	-0,00	2,10	abre a Baño 1, bisagra izq.
—	Paso	1,20 x 2,30	0,00	2,30	
—	Paso	0,90 x 2,30	0,00	2,30	
V01	Ventana	0,80 x 1,25	0,95	2,20	
V02	Ventana	0,80 x 0,80	1,40	2,20	
V03	Ventana	0,45 x 1,35	0,95	2,30	
V04	Ventana	1,20 x 1,25	0,95	2,20	
V05	Ventana	1,70 x 1,10	1,10	2,20	
V06	Ventana	1,60 x 1,35	0,95	2,30	
V07	Ventana	1,80 x 1,25	0,95	2,20	
V08	Ventana	1,80 x 1,25	0,95	2,20	
V09	Ventana	0,90 x 0,80	1,40	2,20	
V10	Ventana	0,90 x 0,80	1,40	2,20	
V11	Ventana	3,10 x 1,25	0,95	2,20	
V12	Ventana	1,70 x 1,10	1,10	2,20	
V13	Ventana	2,20 x 1,80	0,55	2,35	
V14	Ventana	2,60 x 2,20	0,15	2,35	
V15	Ventana	2,60 x 2,20	0,15	2,35	
V16	Ventana	1,60 x 2,20	0,15	2,35	
V17	Ventana	1,00 x 2,20	0,15	2,35	
V18	Ventana	1,40 x 1,25	0,95	2,20	

NPT ±0,00. Fuente: exports/model/casa_v5.FCStd, corte a +1,20 m.
Abatimiento y bisagras: patrón de diseño (R1-R9), sin verificación normativa.
Cortes A-A y B-B: lámina CORTES.
Cotas y niveles en metros. NPT ±0,00.
Sin veredicto normativo: umbrales OGUC sin transcribir (INCONCLUSO).
Norte según el documento rev. G; no hay levantamiento del sitio.

PLANTA PRIMER PISO

Vivienda unifamiliar 2 pisos con patio interior — anteproyecto, versión v5

Propietario: por definir

Arquitecto: por definir Registro: por definir

Dirección: por definir

Rol: por definir Comuna: por definir


Escala 1:50

Papel A2 (594 x 420 mm)

Fecha 2026-10-04 Rev. v5-A

LÁMINA

1 / 6

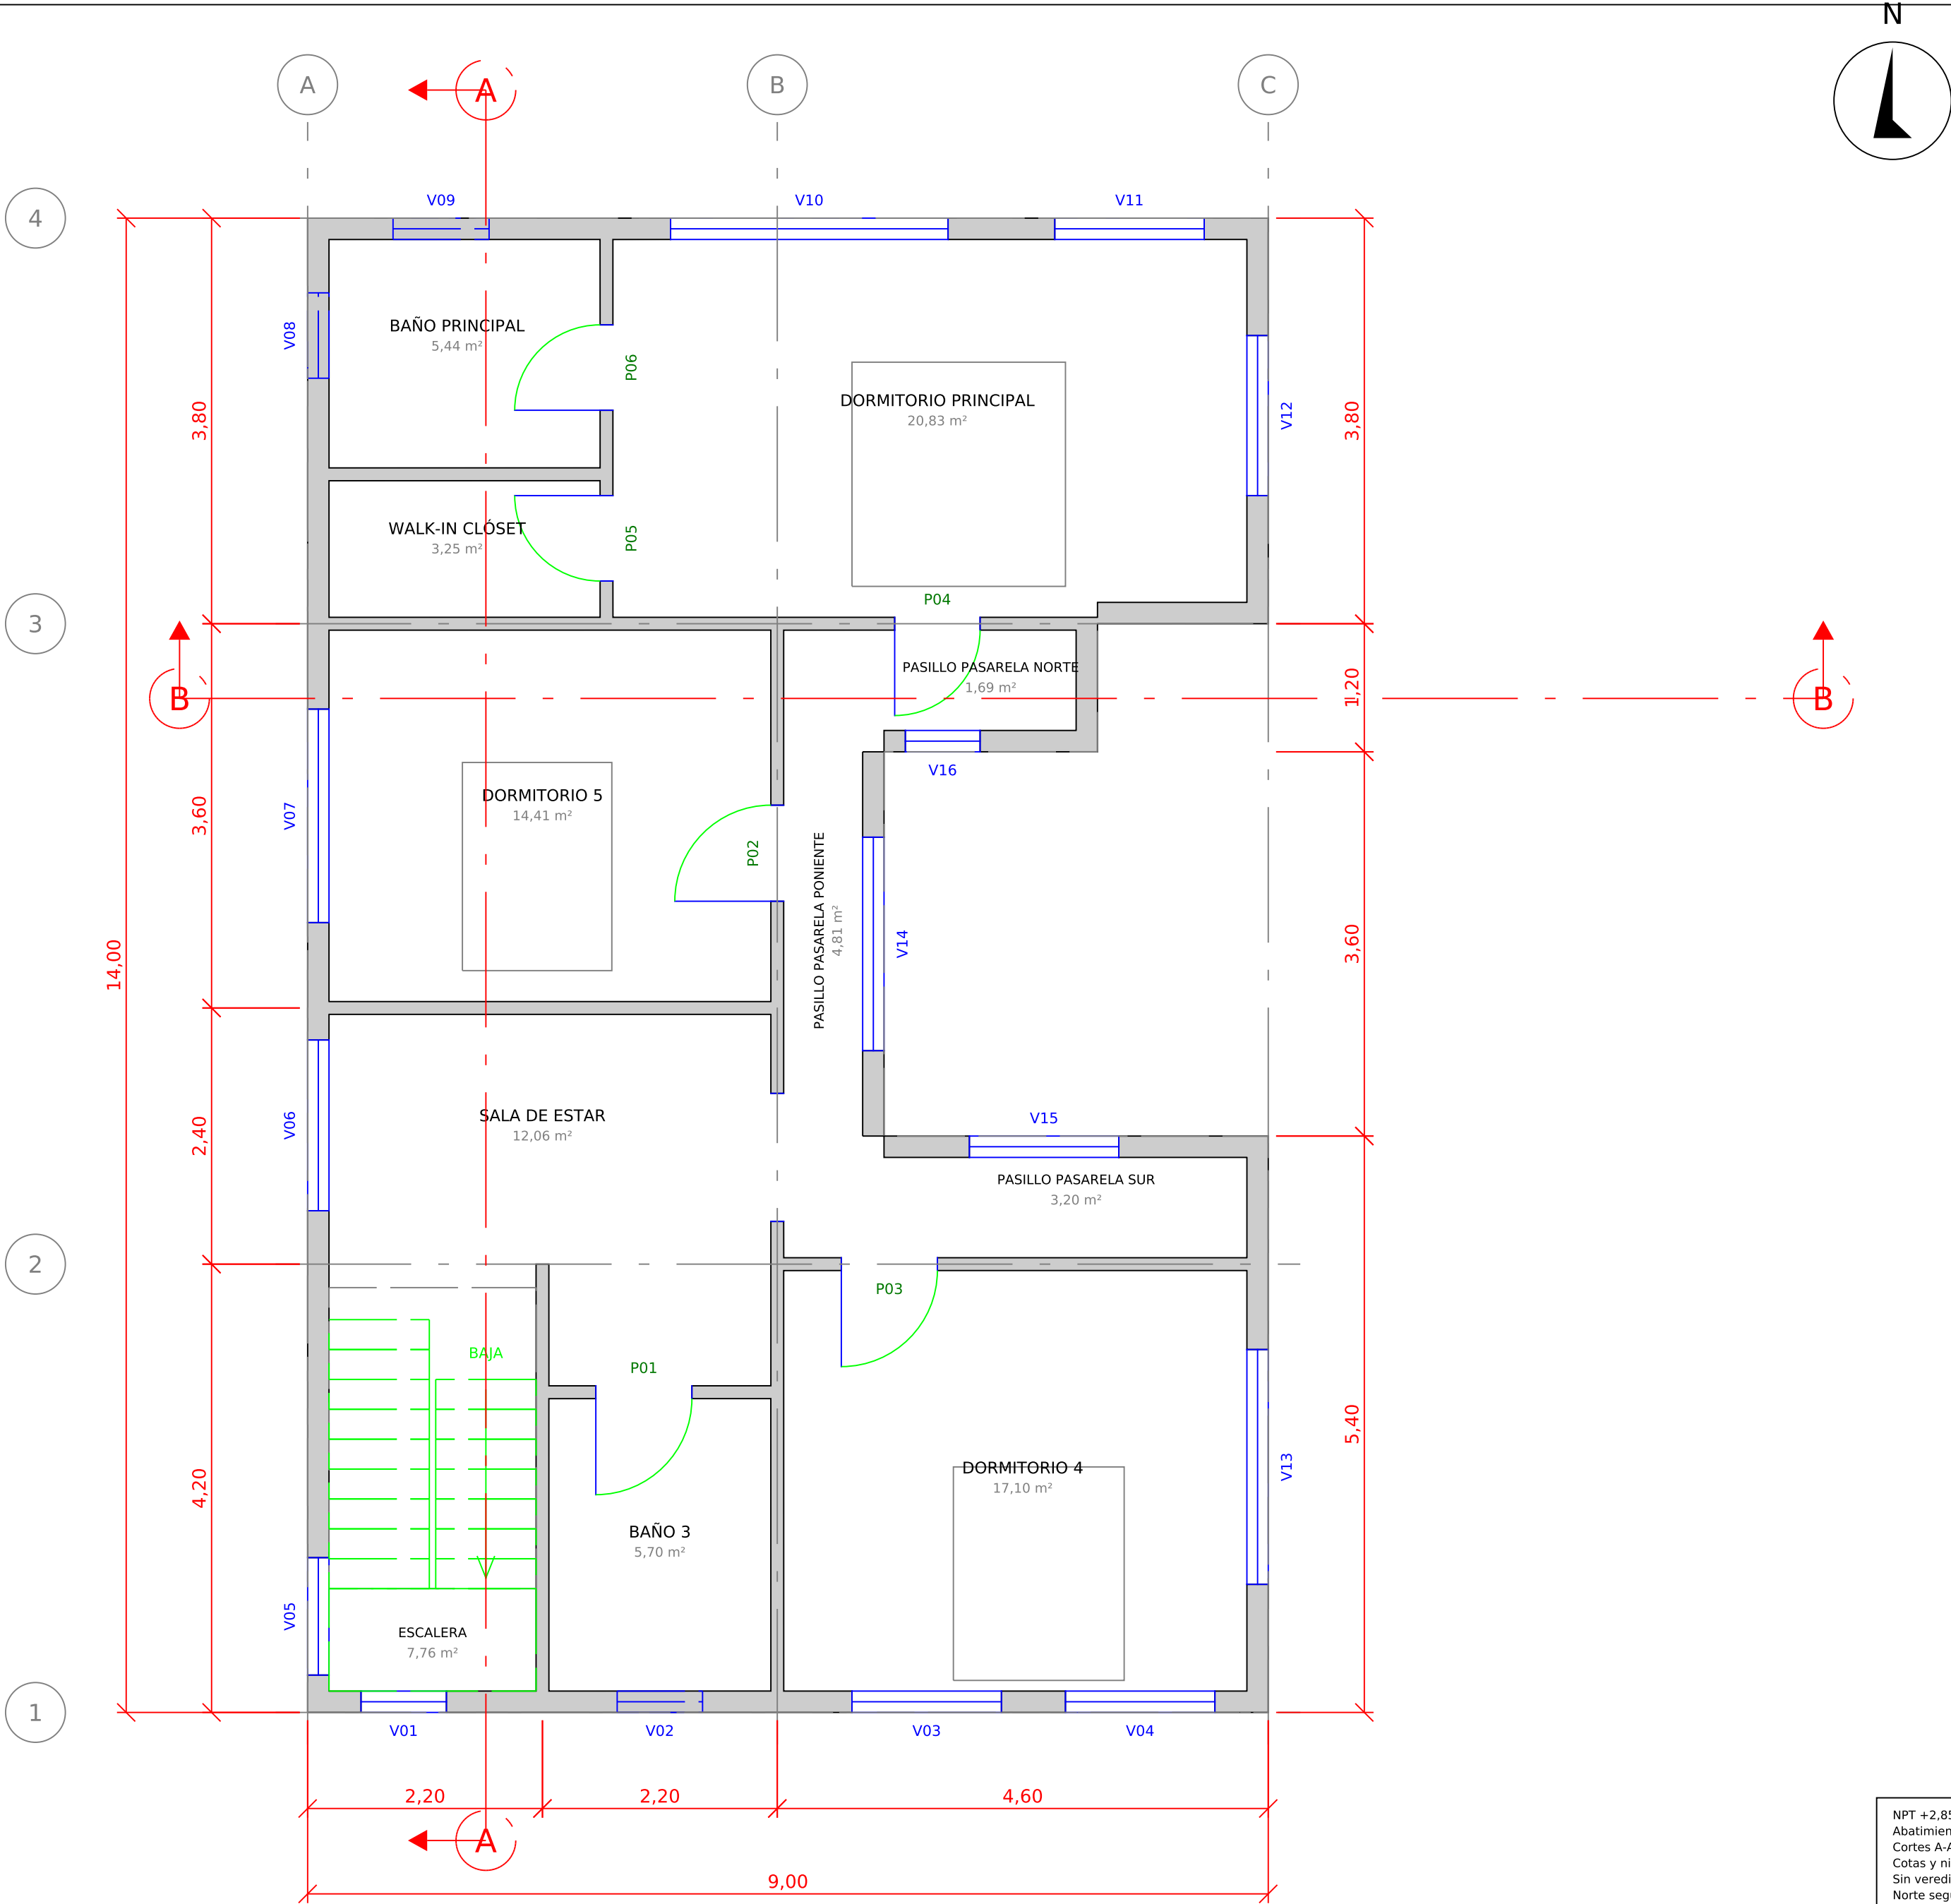

CUADRO DE SUPERFICIES — Segundo Piso

Recinto	A ejes (doc)	Útil (modelo)
Escalera	9,24	7,76
Baño 3	6,60	5,70
Sala de Estar	13,20	12,06
Dormitorio 4	19,32	17,10
Dormitorio 5	15,84	14,41
Pasillo Pasarela Poniente	6,00	4,81
Pasillo Pasarela Sur	4,32	3,20
Pasillo Pasarela Norte	2,40	1,69
Walk-in Clóset	3,92	3,25
Baño Principal	6,72	5,44
Dormitorio Principal	23,56	20,83
Suma recintos interiores	111,12	96,24

A ejes: coincide con el cuadro del documento rev. G (verificado recinto por recinto).
Útil: superficie medida del Space del modelo FreeCAD, descontada la huella de muros.
Exteriores (porche, patios, paso) no suman.

CUADRO DE VANOS



Cód.	Tipo	Ancho x alto	Antepecho	Dintel	Apertura (patrón de diseño)
P01	Puerta	0,90 x 2,10	0,00	2,10	abre a Baño 3, bisagra der.
P02	Puerta	0,90 x 2,10	0,00	2,10	abre a Dormitorio 5, bisagra izq.
P03	Puerta	0,90 x 2,10	0,00	2,10	abre a Dormitorio 4, bisagra der.
P04	Puerta	0,80 x 2,10	0,00	2,10	abre a Pasillo Pasarela Norte, bisagra der.
P05	Puerta	0,80 x 2,10	0,00	2,10	abre a Walk-in Clóset, bisagra der.
P06	Puerta	0,80 x 2,10	0,00	2,10	abre a Baño Principal, bisagra izq.
—	Paso	1,20 x 2,30	0,00	2,30	
V01	Ventana	0,80 x 1,25	0,95	2,20	
V02	Ventana	0,80 x 0,80	1,40	2,20	
V03	Ventana	1,40 x 1,25	0,95	2,20	
V04	Ventana	1,40 x 1,25	0,95	2,20	
V05	Ventana	1,10 x 1,25	0,95	2,20	
V06	Ventana	1,60 x 1,25	0,95	2,20	
V07	Ventana	2,00 x 1,25	0,95	2,20	
V08	Ventana	0,80 x 0,80	1,40	2,20	
V09	Ventana	0,90 x 0,80	1,40	2,20	
V10	Ventana	2,60 x 1,25	0,95	2,20	
V11	Ventana	1,40 x 1,25	0,95	2,20	
V12	Ventana	1,50 x 1,25	0,95	2,20	
V13	Ventana	2,20 x 1,25	0,95	2,20	
V14	Ventana	2,00 x 2,05	0,15	2,20	
V15	Ventana	1,40 x 2,05	0,15	2,20	
V16	Ventana	0,70 x 2,05	0,15	2,20	

NPT +2,85. Fuente: exports/model/casa_v5.FCStd, corte a +1,20 m.
Abatimiento y bisagras: patrón de diseño (R1-R9), sin verificación normativa.
Cortes A-A y B-B: lámina CORTES.
Cotas y niveles en metros. NPT ±0,00.
Sin veredicto normativo: umbrales OGUC sin transcribir (INCONCLUSO).
Norte según el documento rev. G; no hay levantamiento del sitio.

PLANTA SEGUNDO PISO

Vivienda unifamiliar 2 pisos con patio interior — anteproyecto, versión v5
Propietario: por definir
Arquitecto: por definir Registro: por definir
Dirección: por definir
Rol: por definir · Comuna: por definir

Escala 1:50
Papel A2 (594 x 420 mm)
Fecha 2026-10-04 Rev. v5-A
LÁMINA
2 / 6

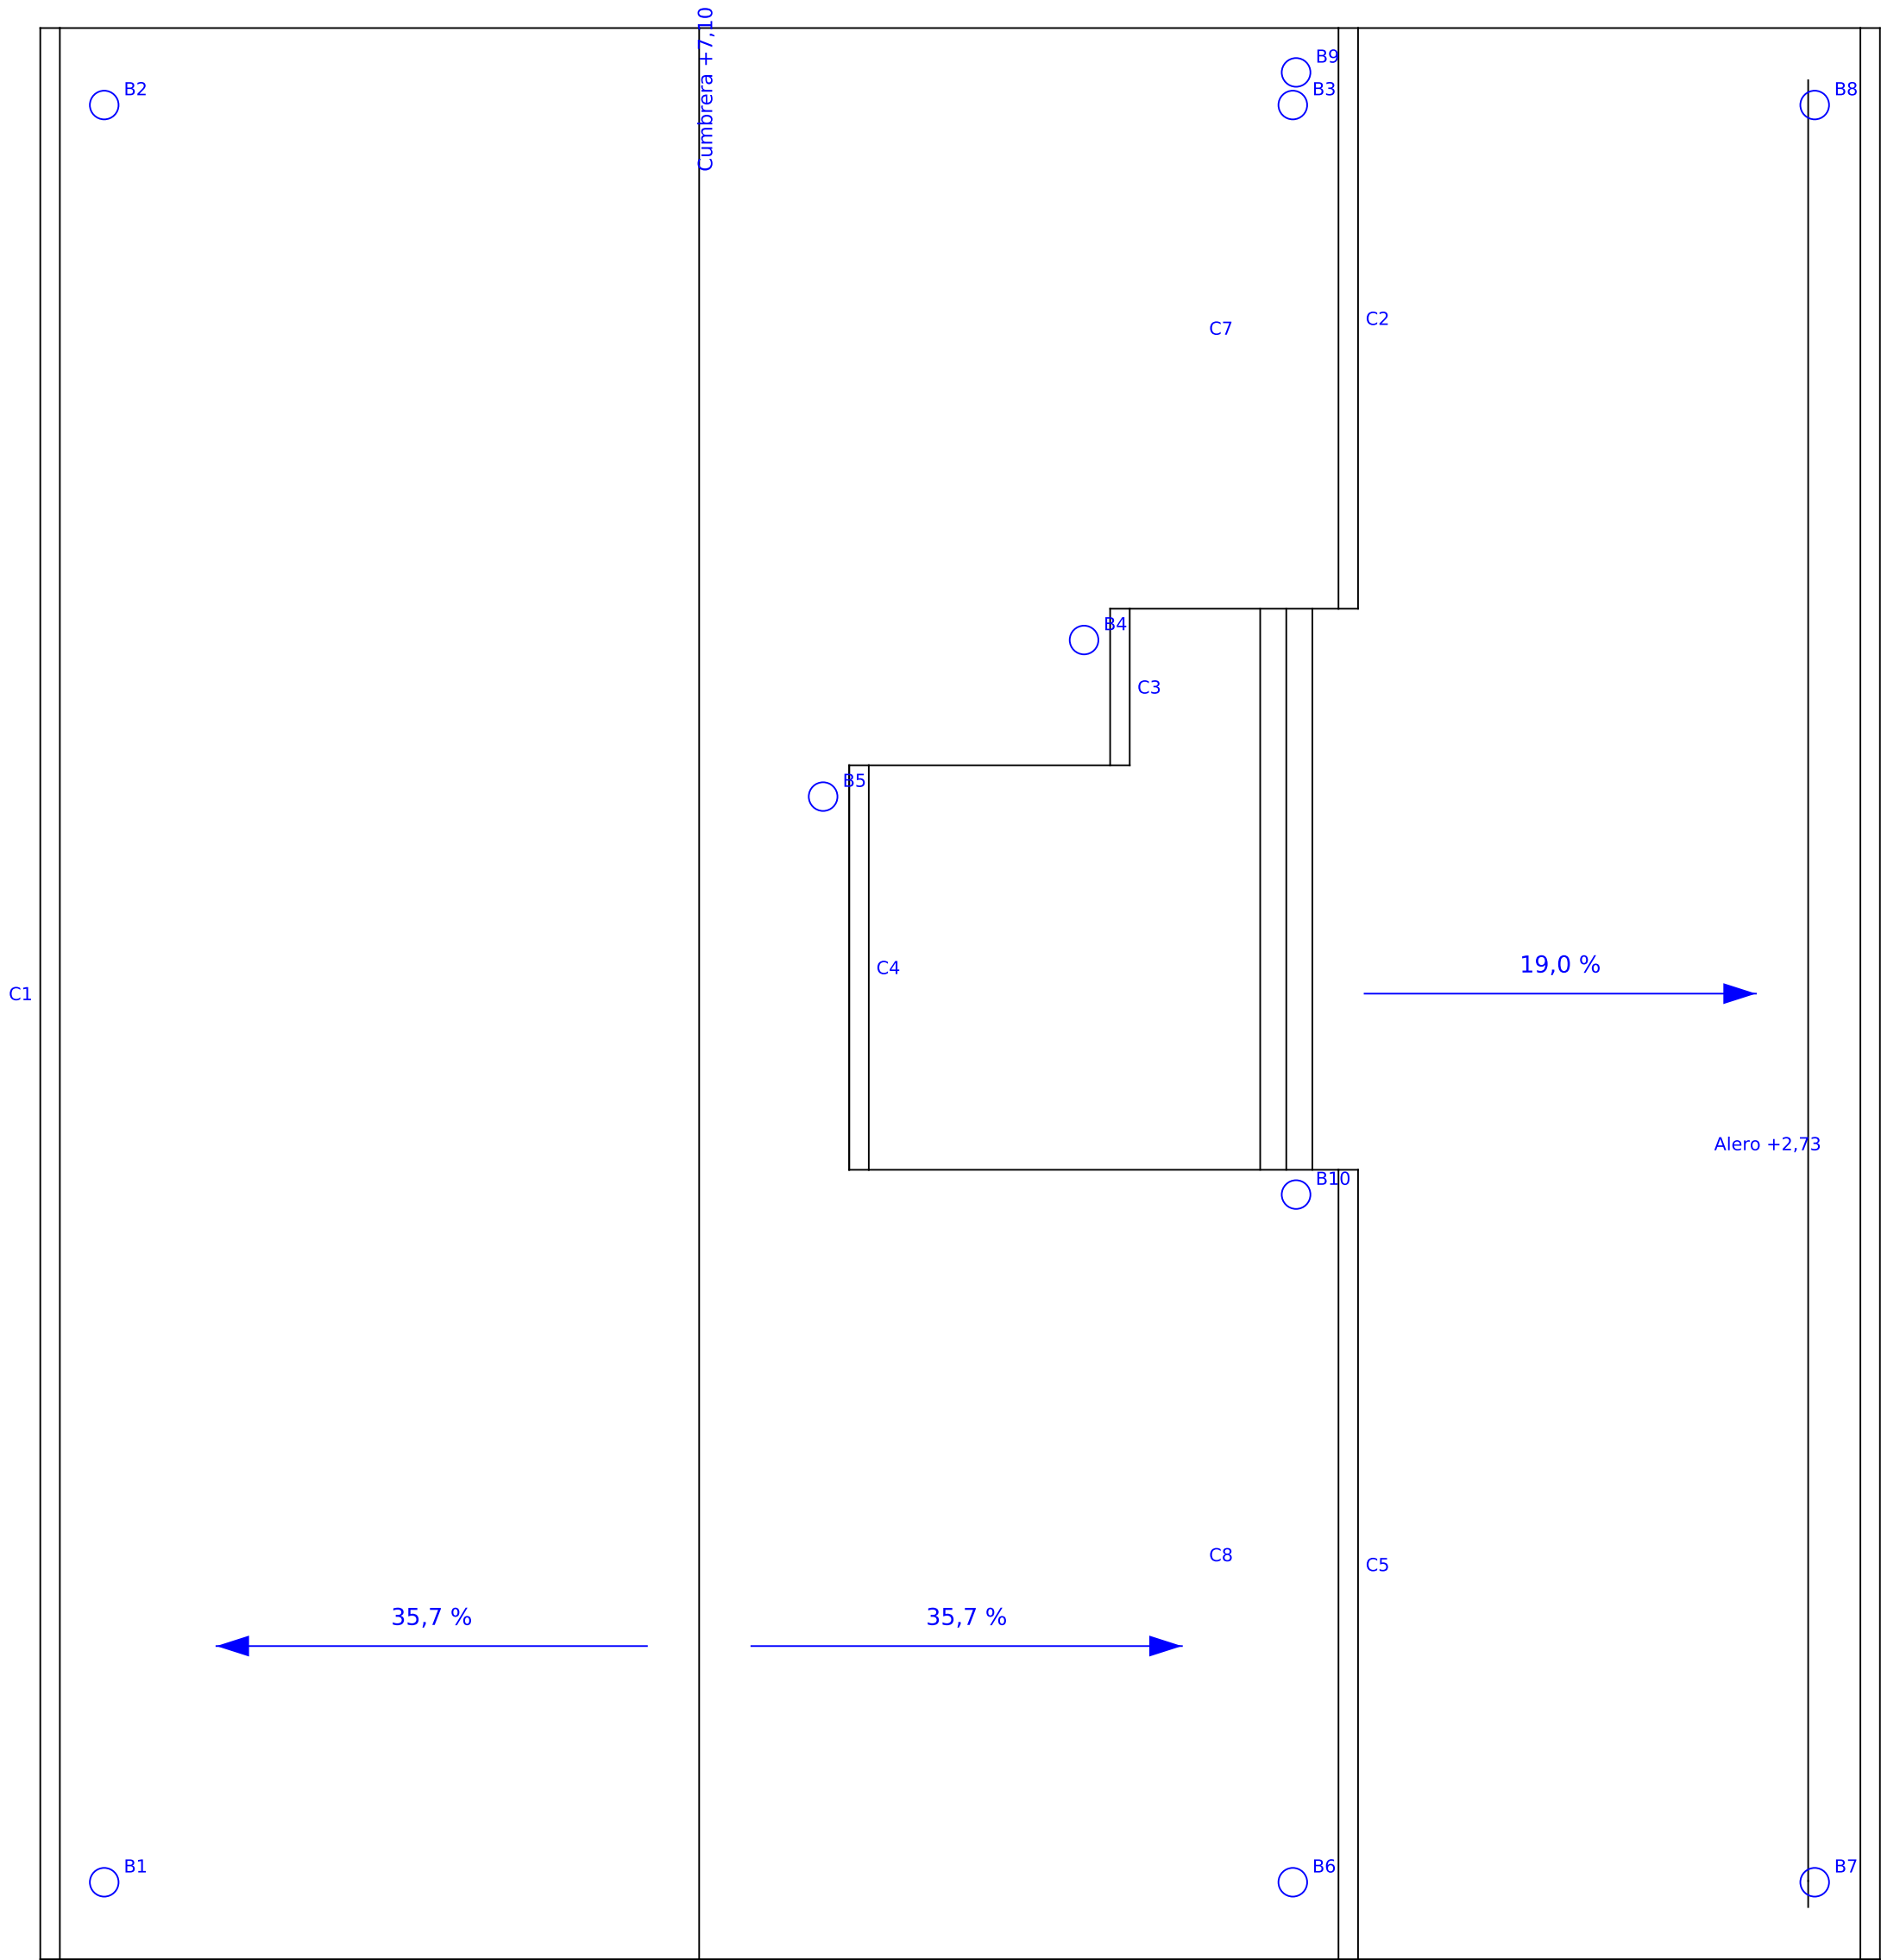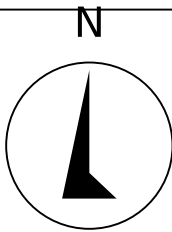

CUADRO DE AGUAS LLUVIAS

Canal	Tipo	Largo m	Área m²	Bajadas	Verificación
C1	alero	14,80	72,52	B1, B2	INCONCLUSO
C2	alero	4,45	21,80	B3	INCONCLUSO
C3	alero	1,20	3,78	B4	INCONCLUSO
C4	alero	3,10	3,56	B5	INCONCLUSO
C5	alero	6,05	29,64	B6	INCONCLUSO
C6	alero	14,80	68,08	B7, B8	INCONCLUSO
C7	encuentro	3,80	3,33	B9	INCONCLUSO
C8	encuentro	5,40	4,73	B10	INCONCLUSO

Canal 150 x 100 mm, bajada 80 mm (convencion); pendiente de canal 0,5 % hacia la bajada.
Encuentro: canal adosado al muro del eje C, con forro y babeta (documento rev. G).
B3 y B6 descargan sobre una cubierta más baja; el resto, a terreno o patio.
Verificación hidráulica INCONCLUSA: falta la intensidad de lluvia de la comuna (site.json) y los parámetros no están transcritos de su fuente oficial.

PLANTA DE CUBIERTA
Escala 1:50


Líneas proyectadas del modelo FreeCAD (vista superior, sin líneas ocultas).
Flechas: escurrimiento; pendiente calculada de cumbrera y alero.
Canales y bajadas: tools/aguas_lluvias.py (agente drainage-designer).
Cotas y niveles en metros. NPT ±0,00.
Sin veredicto normativo: umbrales OGUC sin transcribir (INCONCLUSO).
Norte según el documento rev. G; no hay levantamiento del sitio.

PLANTA DE CUBIERTA

Vivienda unifamiliar 2 pisos con patio interior — anteproyecto, versión v5
Propietario: por definir
Arquitecto: por definir Registro: por definir
Dirección: por definir
Rol: por definir Comuna: por definir


Escala 1:50
Papel A2 (594 x 420 mm)
Fecha 2026-10-04 Rev. v5-A

LÁMINA

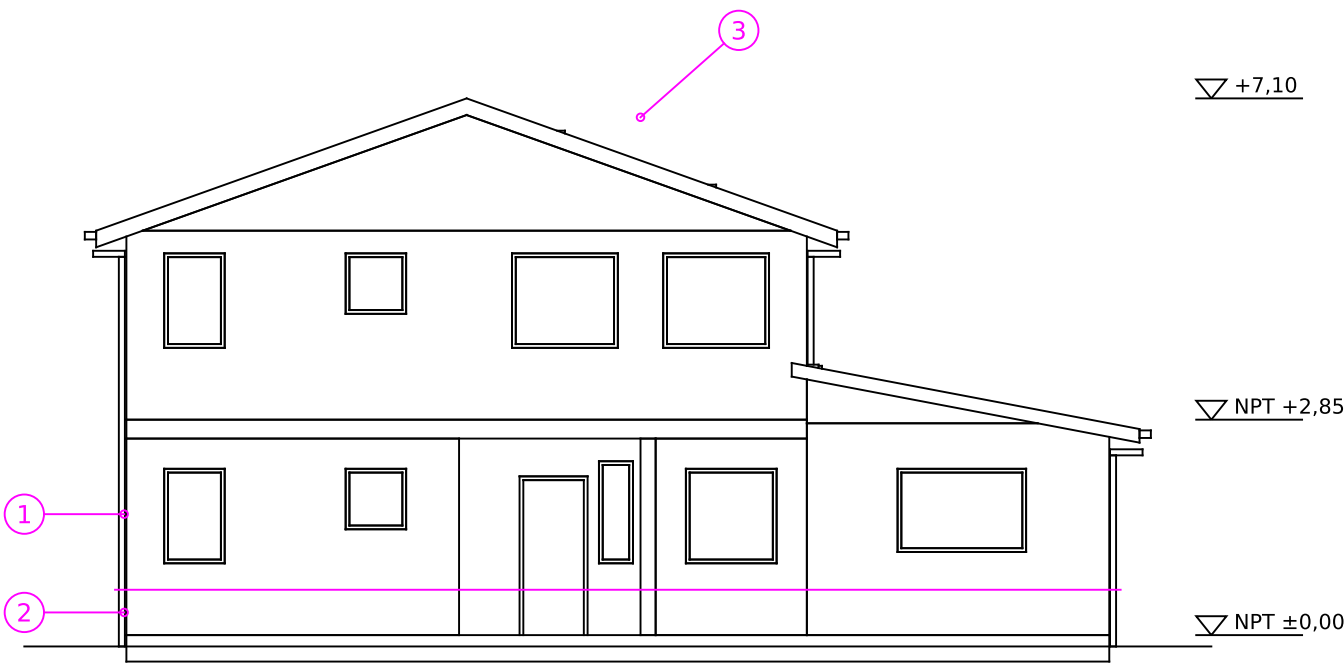


ELEVACIÓN SUR

Escala 1:100

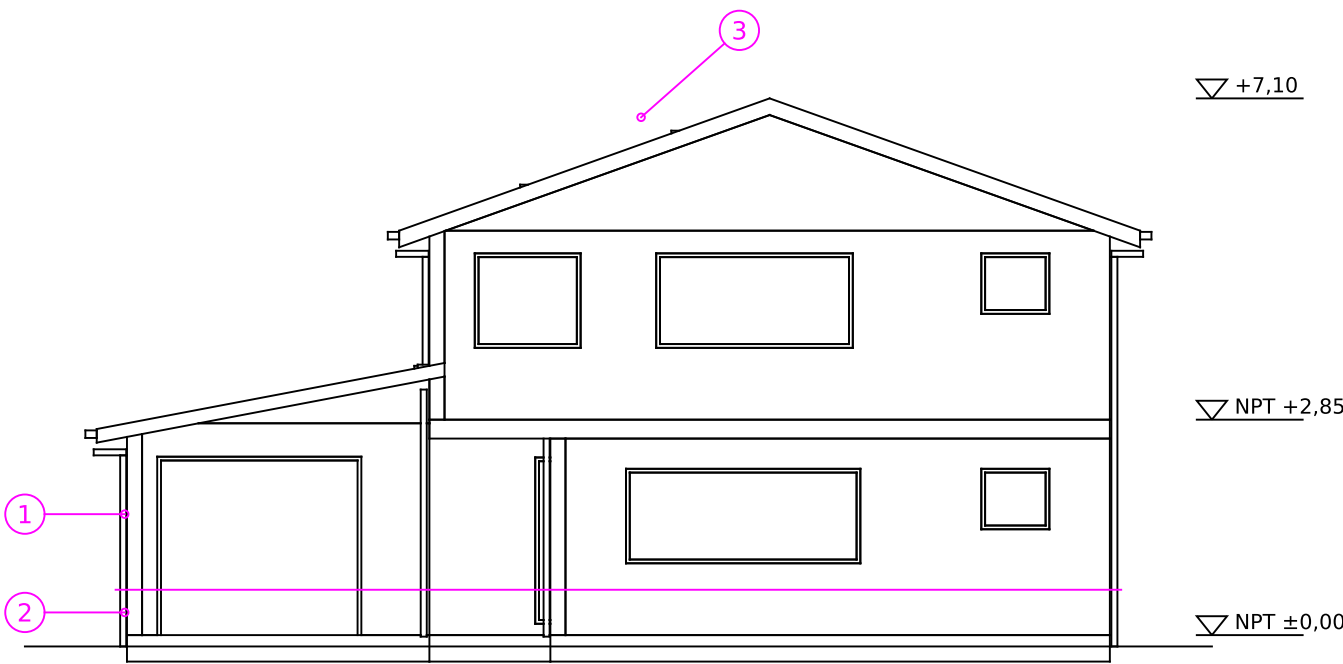


ELEVACIÓN NORTE

Escala 1:100

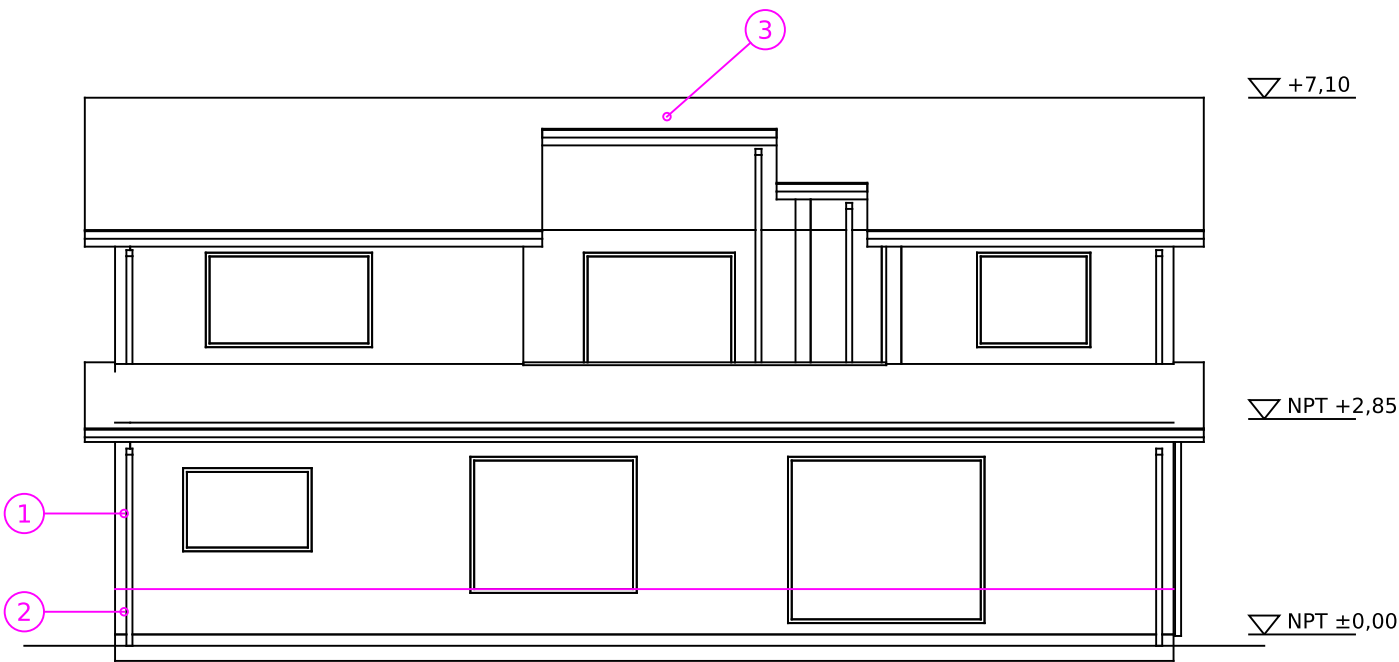

ELEVACIÓN ORIENTE

Escala 1:100

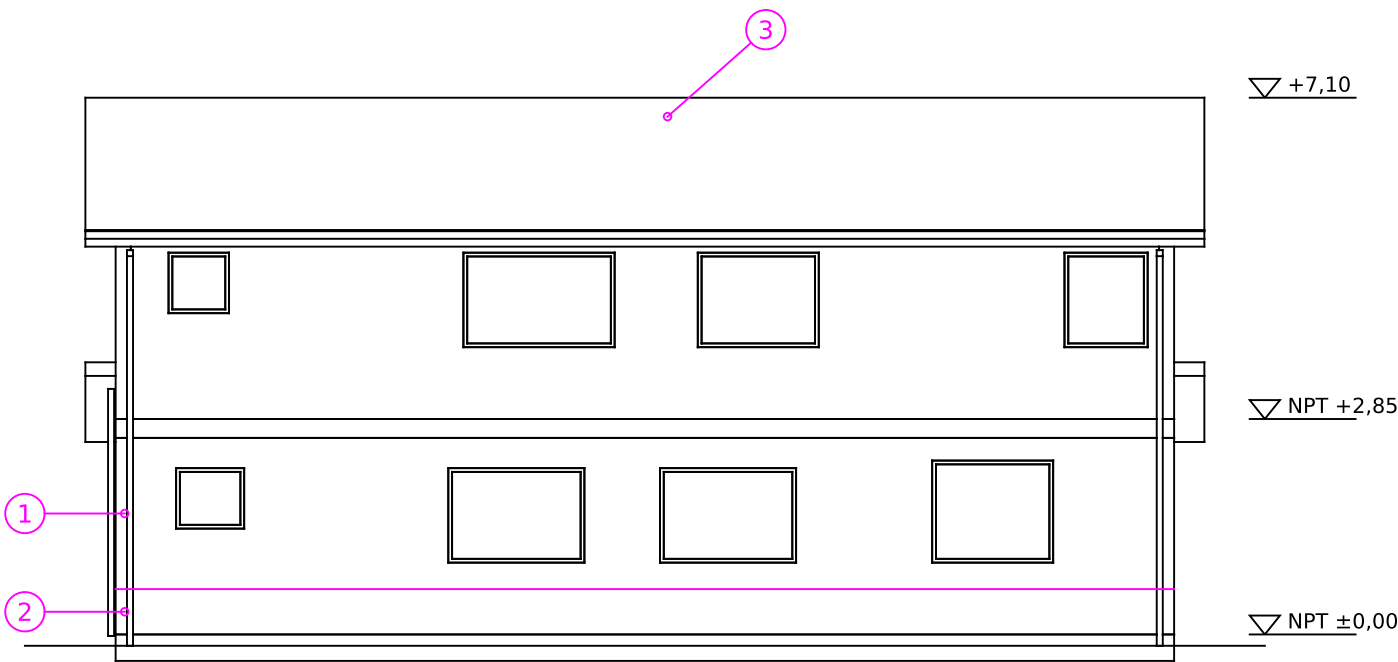

ELEVACIÓN PONIENTE

Escala 1:100

TERMINACIONES DE FACHADA — PROPUESTA, A CONFIRMAR

- Muros exteriores: Estuco de mortero de cemento afinado, pintura elastomérica exterior. Color blanco hueso. [propuesta]
 - Zócalo: Estuco de mortero con hidrófugo, pintura de alto tráfico. Color gris medio. [propuesta]
 - Cubiertas: Plancha de acero prepintado ondulado o trapezoidal sobre fieltro asfáltico y costaneras. Color gris grafito. [propuesta]
 - Aleros y tapacanes: Tapacán y forro de alero en fibrocemento pintado. Color blanco hueso. [propuesta]
 - Canales, bajadas, forros y babetas: Acero prepintado, uniones remachadas y selladas. Color gris grafito. [propuesta]
 - Ventanas y puertas exteriores vidriadas: Perfil de PVC con doble vidriado hermético (termopanel). Color blanco. [propuesta]
 - Puerta de acceso: Puerta de madera sólida con barniz exterior. Color natural. [propuesta]
 - Pavimentos exteriores: Baldosa microvibrada antideslizante sobre radier. Color gris. [propuesta]
- Zócalo: línea a +0,60 m sobre NPT en todas las fachadas.


Elevaciones proyectadas del modelo FreeCAD, sin líneas ocultas.
Terreno a -0,15 (dato del JSON); sin levantamiento del sitio.
Terminaciones: PROPUESTA de facade-designer, a confirmar (source/terminaciones.json).
Cotas y niveles en metros. NPT ±0,00.
Sin veredicto normativo: umbrales OGUC sin transcribir (INCONCLUSO).
Norte según el documento rev. G; no hay levantamiento del sitio.

ELEVACIONES

Vivienda unifamiliar 2 pisos con patio interior — anteproyecto, versión v5
Propietario: por definir
Arquitecto: por definir Registro: por definir
Dirección: por definir
Rol: por definir · Comuna: por definir

Escala 1:100


Papel A2 (594 x 420 mm)
Fecha 2026-10-04 Rev. v5-A
LÁMINA

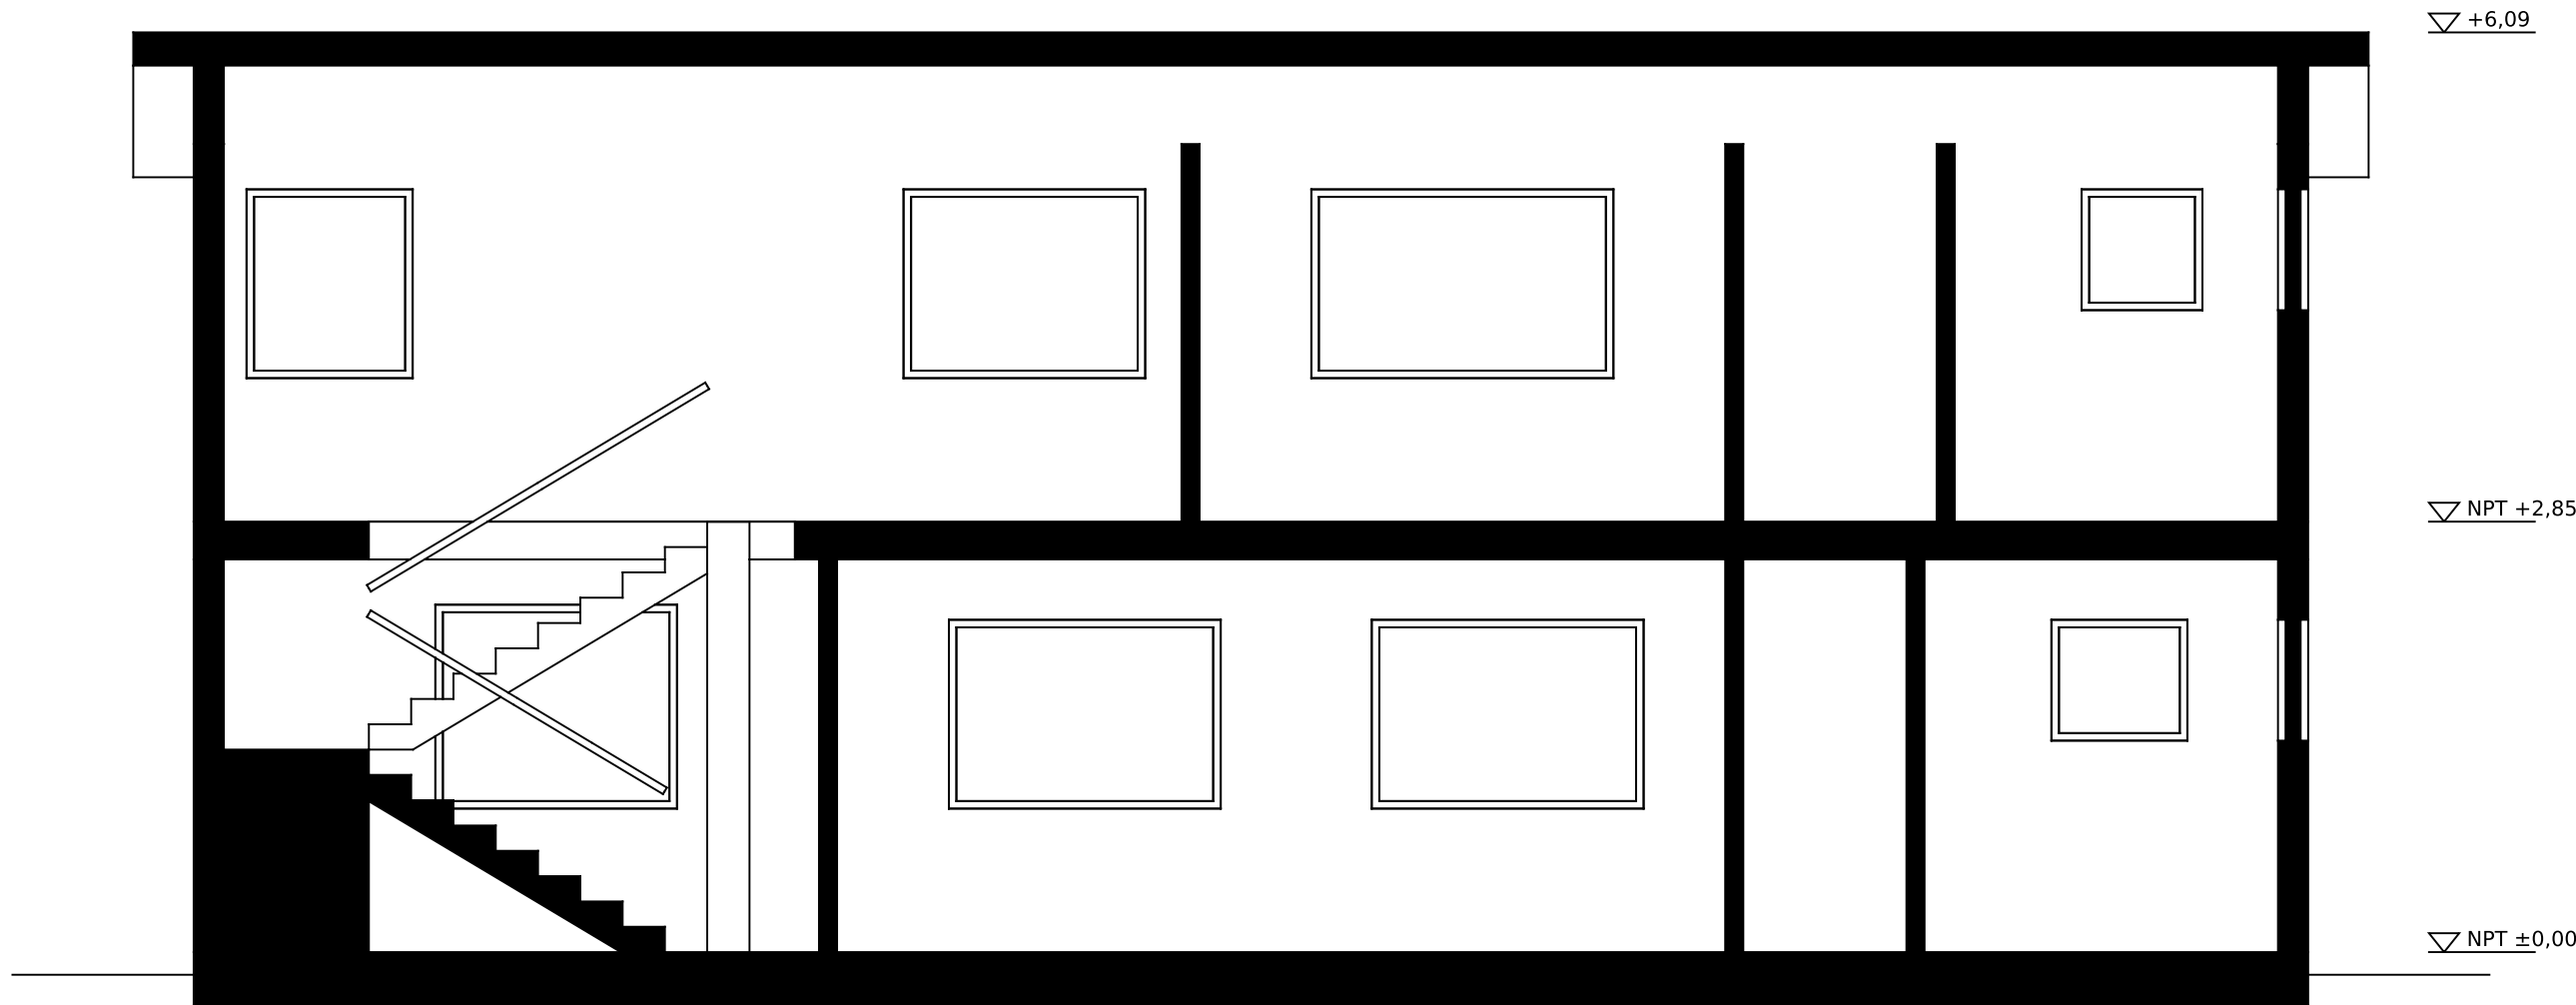

CORTE A-A

Escala 1:50

Plano X = 1,67 m, mirando al poniente

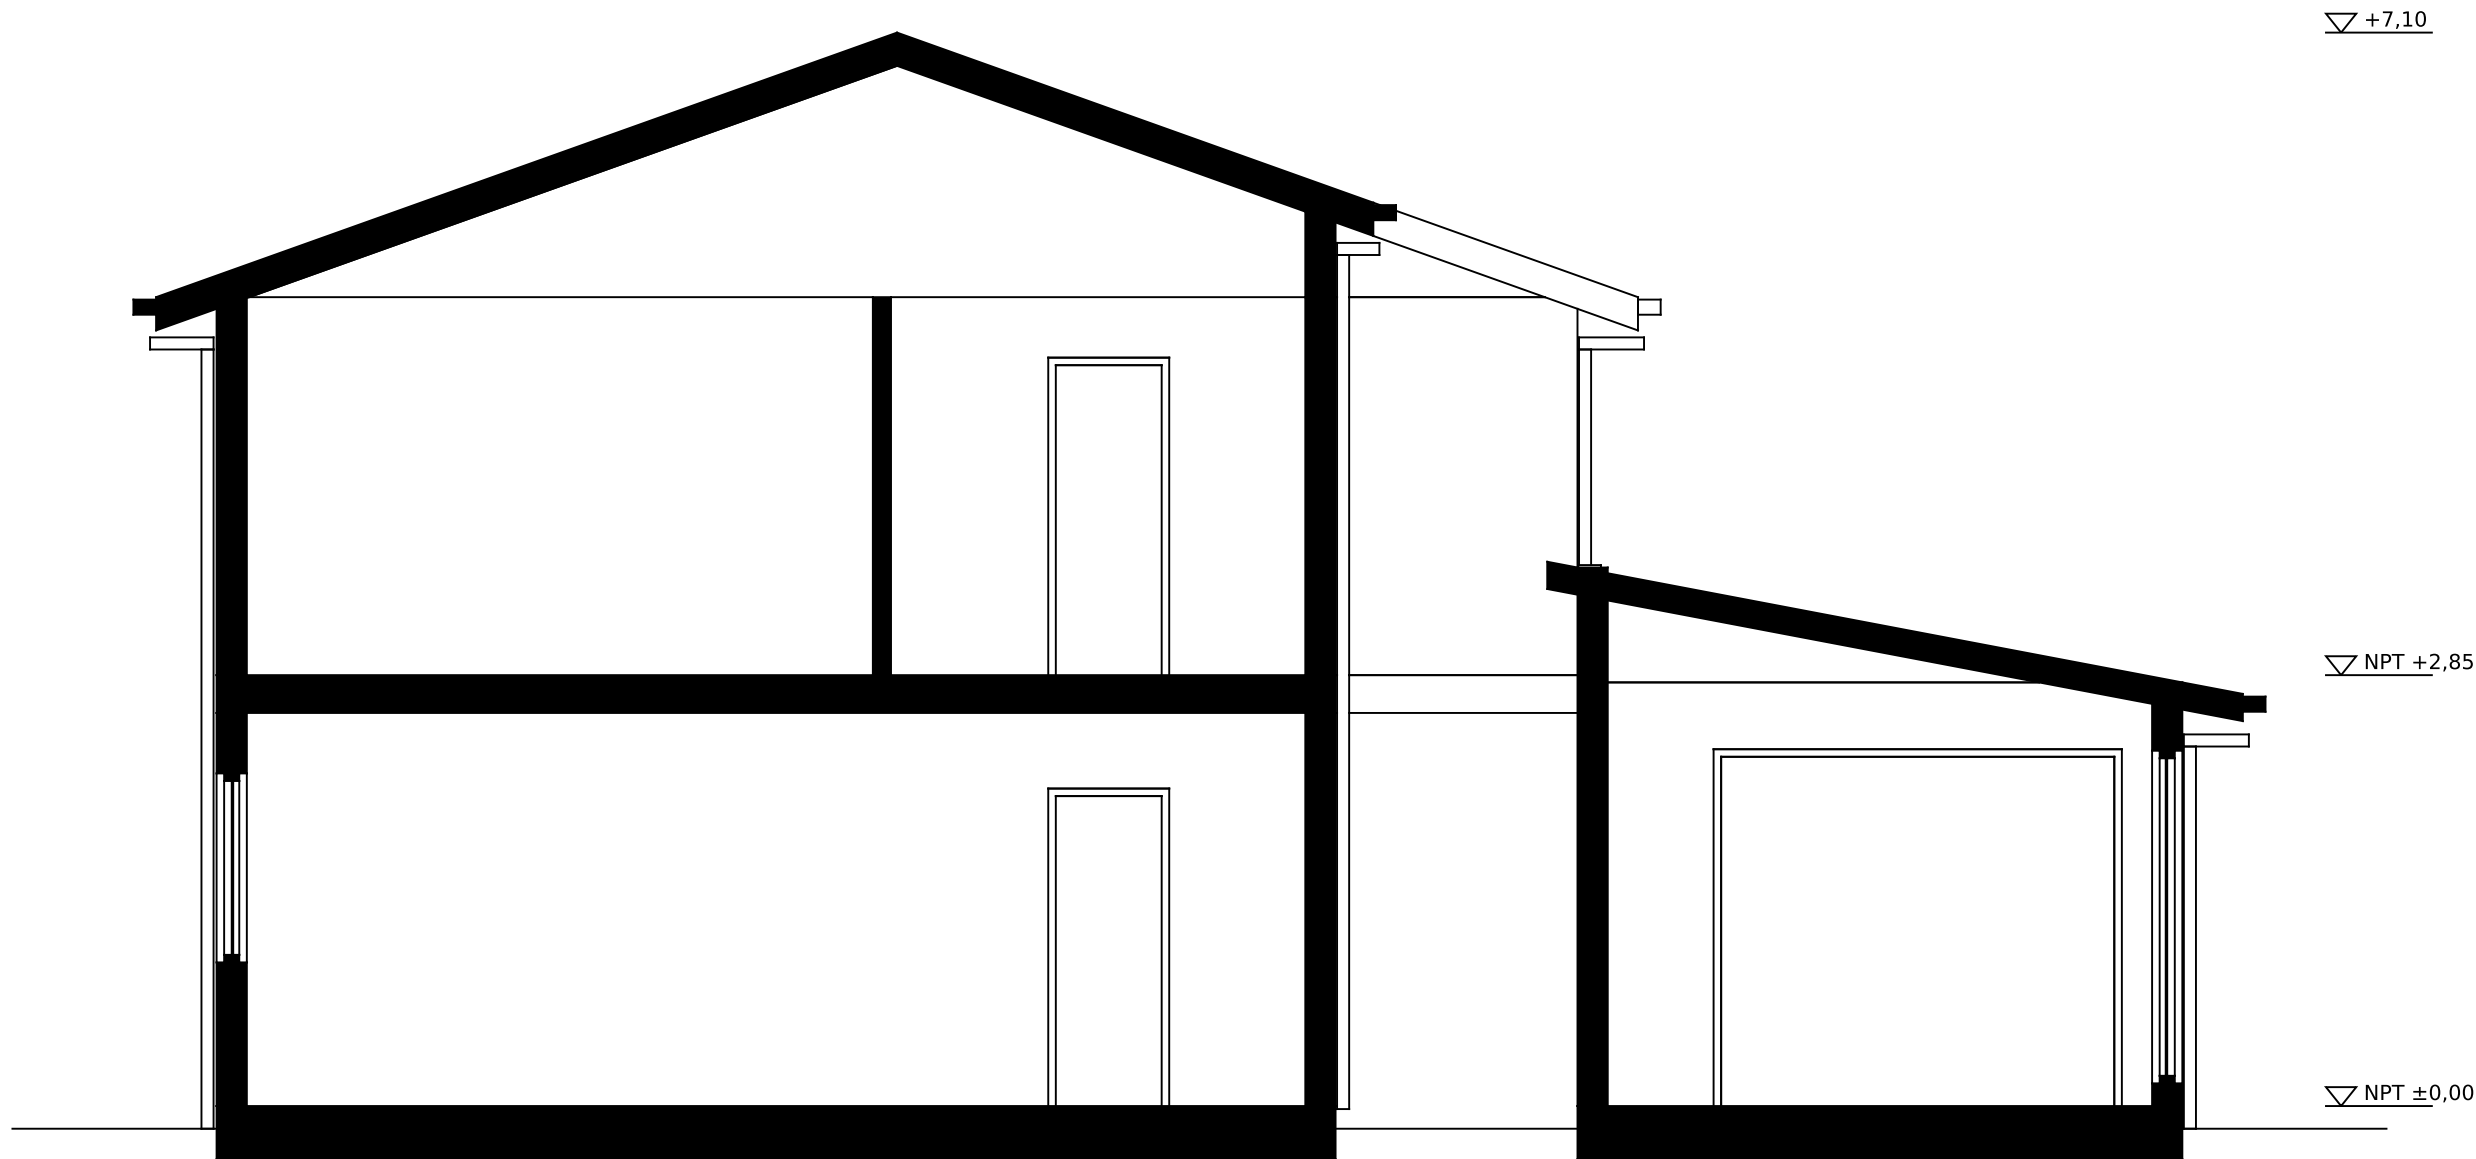

CORTE B-B

Escala 1:50

Plano Y = -4,50 m, mirando al norte

Cortes del modelo FreeCAD; en gris, lo que corta el plano (poché).
Ubicación de A-A y B-B: líneas de corte en las plantas.
Holgura de escalera 1,259 m; hallazgo abierto (README de v2).
Cotas y niveles en metros. NPT ±0,00.
Sin veredicto normativo: umbrales OGUC sin transcribir (INCONCLUSO).
Norte según el documento rev. G; no hay levantamiento del sitio.

CORTES A-A Y B-B

Vivienda unifamiliar 2 pisos con patio interior — anteproyecto, versión v5

Propietario: por definir

Arquitecto: por definir Registro: por definir

Dirección: por definir

Rol: por definir · Comuna: por definir

Escala 1:50

Papel A2 (594 x 420 mm)

Fecha 2026-10-04 Rev. v5-A

LÁMINA

5 / 6



6 / 6