

4

3

2

1

A

B

C

D



CUADRO DE SUPERFICIES — Primer Piso

Recinto	A área (doc)	GBL (modelo)
Escalera	9.24	7.64
Baño 2	4.62	2.57
Hall Escalera	4.62	3.84
Hall de Acceso	6.48	6.00
Logia	9.24	7.68
Porche (ext.)	3.60	3.60
Escalero Libre	17.40	15.98
Pasillo Galería Poniente	6.00	5.16
Pasillo Galería Sur	6.12	4.94
Pasillo Galería Norte	4.20	3.10
Closet	3.12	2.53
Baño 1	6.76	5.40
Dormitorio 1	18.24	16.07
Cocina	15.60	13.10
Comedor	14.80	13.10
Living	22.60	22.32
Patio Interior (ext.)	18.36	18.36
Paseo Cubierto (ext.)	6.08	6.08
Paseo Descubierta (ext.)	1.92	1.92
Suma recintos interiores	152.04	130.61

A área coincide con el cuadro del documento rev. 0 (verificado recibo por recinto).
GBL superficie medida del Sapo de masivos FreeCAD, decorados la huella de muro.
Exteriores (puerto, patio, pasillo no surten).

CUADRO DE VAMOS

Cid.	Tipo	Ancho x alto	Antespecho	Dintel	Apertura (patrón de diseño)
P01	Puerta	0.90 x 2.10	-0.00	2.10	alere a Hall de Acceso, loggia der.
P02	Puerta	2.10 x 2.35	-0.00	2.35	comodera
P03	Puerta	2.00 x 2.35	-0.00	2.35	comodera
P04	Puerta	0.90 x 2.10	-0.00	2.10	alere a Patio interior, loggia der.
P05	Puerta	0.90 x 2.10	-0.00	2.10	2 traves a Paseo Cubierta, loggia surten
P06	Puerta	0.90 x 2.10	-0.00	2.10	alere a Hall de Acceso, loggia der.
P07	Puerta	0.90 x 2.10	-0.00	2.10	alere a Baño 2, loggia der.
P08	Puerta	0.90 x 2.10	-0.00	2.10	alere a Logia, loggia der.
P09	Puerta	0.90 x 2.10	-0.00	2.10	alere a Logia, loggia der.
P10	Puerta	0.90 x 2.10	-0.00	2.10	alere a Dormitorio 1, loggia der.
P11	Puerta	0.90 x 2.10	-0.00	2.10	alere a Closet, loggia der.
P12	Puerta	0.90 x 2.10	-0.00	2.10	alere a Baño 1, loggia der.
-	Paseo	2.20 x 2.50	0.00	2.50	
V01	Ventana	0.80 x 1.25	0.95	2.20	
V02	Ventana	0.80 x 0.80	1.40	2.20	
V03	Ventana	0.85 x 1.35	0.95	2.30	
V04	Ventana	1.20 x 1.25	0.95	2.20	
V05	Ventana	1.10 x 1.10	1.10	2.20	
V06	Ventana	1.40 x 1.35	0.95	2.30	
V07	Ventana	1.80 x 1.25	0.95	2.20	
V08	Ventana	1.80 x 1.25	0.95	2.20	
V09	Ventana	0.90 x 0.80	1.40	2.20	
V10	Ventana	0.90 x 0.80	1.40	2.20	
V11	Ventana	1.30 x 1.25	0.95	2.20	
V12	Ventana	1.70 x 1.10	1.10	2.20	
V13	Ventana	1.30 x 1.80	0.95	2.35	
V14	Ventana	2.80 x 2.20	0.15	2.35	
V15	Ventana	1.80 x 2.20	0.15	2.35	
V16	Ventana	1.80 x 2.20	0.15	2.35	
V17	Ventana	1.80 x 2.20	0.15	2.35	
V18	Ventana	1.40 x 1.25	0.95	2.20	

PLANTA PRIMER PISO


Vivienda unifamiliar 2 pisos con patio interior — anteproyecto, v2 (reconstruida desde rev. Gm)
Escala: 1:50 (A2) — Calas en metros — NPT: ±0.00


Fuente:
Comuna, no y PRC: por definir (este paso)
Norte según el documento rev. 0, no hay levantamiento del sitio

Abastecimiento y biogas: patrón de diseño (P2, P3), sin verificación normativa
Sin verificación normativa: umbrales OGUC sin transitorio (INCORUGOS)
Fecha 2020-10-01 Rev. v2-A

PLANTA PRIMER PISO

1:50

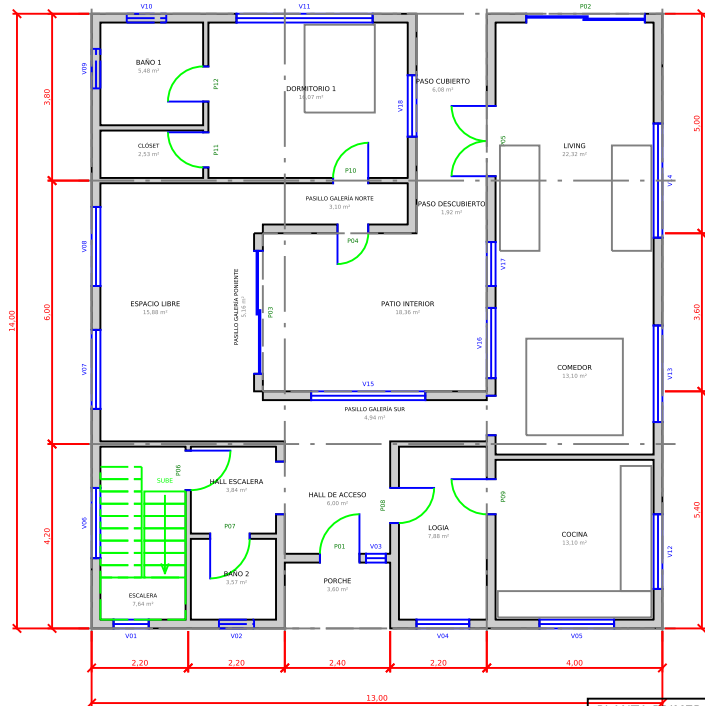

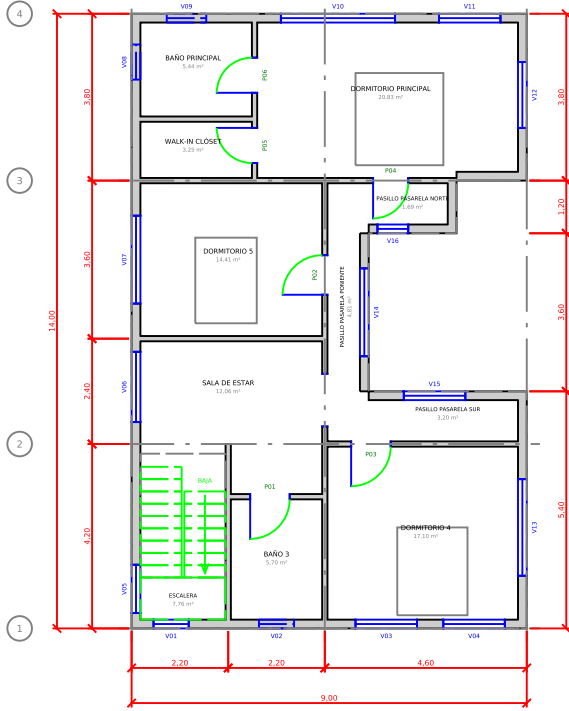

PLANTA SEGUNDO PISO
1:50

NPT +2.85



CUADRO DE SUPERFICIES — Segundo Piso

Ruizinto	A ejes (doc)	GBI (modelo)
Escalera	9.24	7.76
Baño 2	6.60	5.70
Sala de Estar	13.20	12.06
Dormitorio 4	19.32	17.10
Dormitorio 5	15.84	14.41
Pasillo Pasarela Poniente	6.00	4.81
Pasillo Pasarela Sur	4.32	3.20
Pasillo Pasarela Norte	2.40	1.60
Walk-in Closet	3.92	3.25
Baño Principal	6.72	5.44
Dormitorio Principal	23.56	20.83
Suma recintos interiores	111.12	96.24

A: ejes, cancela del eje cancela del documento rev. G, certificado recibo por recibo.
(GBI) superficie medida del Espacio del modelo Proyectado, descontada la huella de muro.
Enteros (cancela, patio, jardín) en sumas.

CUADRO DE VANOS

Cód.	Tipo	Ancho x alto	Anteproyecto	Detalle	Apertura (patrón de diseño)
P01	Puerta	0.90 x 2.10	0.00	2.10	alre a Baño 3, bisagra der.
P02	Puerta	0.90 x 2.10	0.00	2.10	alre a Dormitorio 5, bisagra izq.
P03	Puerta	0.90 x 2.10	0.00	2.10	alre a Dormitorio 4, bisagra der.
P04	Puerta	0.80 x 2.10	0.00	2.10	alre a Pasillo Pasarela Norte, bisagra der.
P05	Puerta	0.80 x 2.10	0.00	2.10	alre a Walk-in Closet, bisagra der.
P06	Puerta	0.80 x 2.10	0.00	2.10	alre a Baño Principal, bisagra izq.
—	Fijado	1.20 x 2.30	0.00	2.30	
V01	Ventana	0.80 x 1.25	0.95	2.20	
V02	Ventana	0.80 x 0.80	1.40	2.20	
V03	Ventana	1.40 x 1.25	0.95	2.20	
V04	Ventana	1.40 x 1.25	0.95	2.20	
V05	Ventana	1.30 x 1.25	0.95	2.20	
V06	Ventana	1.40 x 1.25	0.95	2.20	
V07	Ventana	2.00 x 1.25	0.95	2.20	
V08	Ventana	0.80 x 0.80	1.40	2.20	
V09	Ventana	0.90 x 0.80	1.40	2.20	
V10	Ventana	2.40 x 1.25	0.95	2.20	
V11	Ventana	2.40 x 1.25	0.95	2.20	
V12	Ventana	1.50 x 1.25	0.95	2.20	
V13	Ventana	2.00 x 1.25	0.95	2.20	
V14	Ventana	2.00 x 2.00	0.15	2.20	
V15	Ventana	1.40 x 2.00	0.15	2.20	
V16	Ventana	0.70 x 2.00	0.15	2.20	

PLANTA SEGUNDO PISO

Vivienda unifamiliar 2 pisos con patio interior — anteproyecto, v2 (reconstruida desde rev. GH)
Escala: 1:50 (A2) — Cortes en metros — NPT +2.85

Fuente: x2bqgsm/modelluam_v2_FCHS (objetos Archi), cortes a +1.20 m
Comuna, no y RUC: por definir (este plano)
Norte según el documento rev. G; no hay levantamiento del sitio

Abastecimiento y biogas: patrón de diseño (P1, P2), sin verificación normativa
Sin verificado normativo: umbrales OGC (sin transitorio (MCONC/USO))
Fecha 2020-10-01 Rev. v-A