


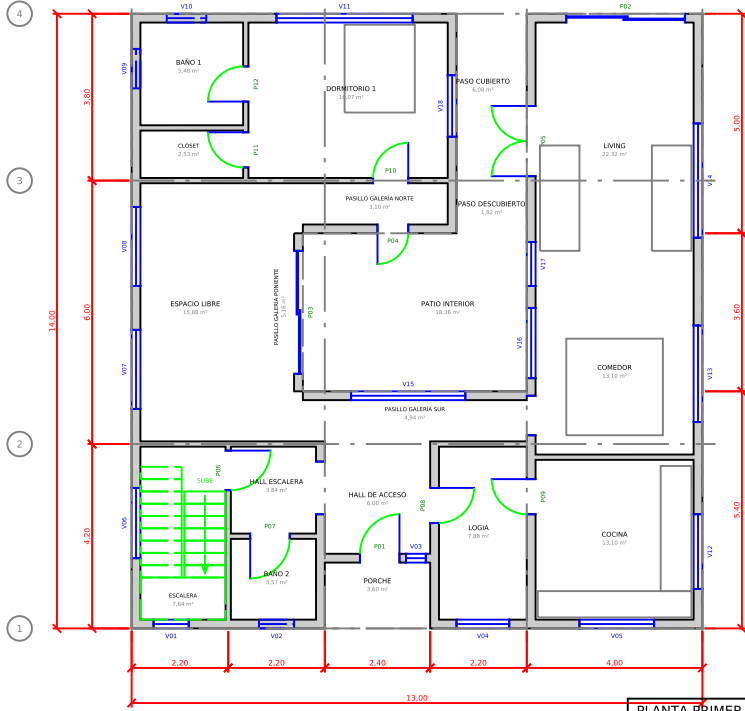

PLANTA PRIMER PISO
1:50



CUADRO DE SUPERFICIES — Primer Piso

Recinto	A ejes (doc)	GBI (modelo)
Escalera	9.24	7.64
Baño 2	4.62	2.57
Hall Escalera	4.62	3.84
Hall de Acceso	6.48	6.00
Logia	9.24	7.68
Porche (ext.)	3.60	3.60
Espacio Libre	17.40	15.98
Pasillo Galeria Poniente	6.00	5.16
Pasillo Galeria Sur	6.12	4.94
Pasillo Galeria Norte	4.20	3.10
Closet	3.12	2.53
Baño 1	6.76	5.40
Dormitorio 1	18.24	16.07
Cocina	15.60	13.10
Comedor	14.80	13.10
Living	22.60	22.32
Patio Interior (ext.)	18.36	18.36
Paseo Cubierto (ext.)	6.08	6.08
Paseo Descubierta (ext.)	1.92	1.92
Suma recintos interiores	152.04	130.61

A ejes coincide con el cuadro del documento rev. 0 (verificado recibo por recinto).
GBI: superficie medida en Space de modelo FreeCad, decorados la huella de muros.
Exteriores (porche, patio, paseo no surten).

CUADRO DE VANOS


Cid.	Tipo	Ancho x alto	Antepecho	Dintel	Apertura (patrón de diseño)
P01	Puerta	0.90 x 2.10	-0.00	2.10	alene a Hall de Acceso, loggia del comedor.
P02	Puerta	2.10 x 2.35	-0.00	2.35	comedero.
P03	Puerta	2.00 x 2.35	-0.00	2.35	alene a Patio interior, loggia del comedor.
P04	Puerta	0.90 x 2.10	-0.00	2.10	alene a Pasillo interior, loggia del comedor.
P05	Puerta	1.40 x 2.35	-0.00	2.35	alene a Pasillo interior, loggia del comedor.
P06	Puerta	0.90 x 2.10	-0.00	2.10	alene a Baño 2, loggia del comedor.
P07	Puerta	0.90 x 2.10	-0.00	2.10	alene a Baño 2, loggia del comedor.
P08	Puerta	0.90 x 2.10	-0.00	2.10	alene a Logia, loggia del comedor.
P09	Puerta	0.80 x 2.10	-0.00	2.10	alene a Dormitorio 1, loggia del comedor.
P10	Puerta	0.80 x 2.10	-0.00	2.10	alene a Dormitorio 1, loggia del comedor.
P11	Puerta	0.80 x 2.10	-0.00	2.10	alene a Closet, loggia del comedor.
P12	Puerta	0.80 x 2.10	-0.00	2.10	alene a Baño 1, loggia del comedor.
V01	Paseo	2.20 x 2.50	0.00	2.50	
V02	Paseo	0.90 x 2.50	0.00	2.50	
V03	Ventana	0.80 x 1.25	0.95	2.20	
V04	Ventana	0.80 x 0.80	1.40	2.20	
V05	Ventana	0.45 x 1.35	0.95	2.30	
V06	Ventana	1.20 x 1.25	0.95	2.20	
V07	Ventana	1.10 x 1.10	1.10	2.20	
V08	Ventana	1.40 x 1.35	0.95	2.30	
V09	Ventana	1.80 x 1.25	0.95	2.20	
V10	Ventana	1.80 x 1.25	0.95	2.20	
V11	Ventana	0.90 x 0.80	1.40	2.20	
V12	Ventana	0.90 x 0.80	1.40	2.20	
V13	Ventana	1.70 x 1.10	1.10	2.20	
V14	Ventana	2.30 x 1.80	0.95	2.35	
V15	Ventana	2.80 x 2.20	0.15	2.35	
V16	Ventana	1.80 x 2.20	0.15	2.35	
V17	Ventana	1.80 x 2.20	0.15	2.35	
V18	Ventana	1.40 x 1.25	0.95	2.20	

PLANTA PRIMER PISO

Vivienda unifamiliar 2 pisos con patio interior — anteproyecto, v3 (reconstruida desde source/Text)
Escala: 1:50 (A2) — Cotas en metros — NPT: ±0.00

Fuente: «\shared\proyectos\modulos\1\3\FCHB Archi, cinto a 1.20 m
Comuna, no y PRC: por definir (este punto)
Nota: según el documento rev. 0, no hay levantamiento del sitio

Abastecimiento y biogas: patrón de diseño (P2, P3, sin verificación normativa
Sin verificación normativa: umbrales OGUC sin transitorio (INCORUGO)
Fecha: 2024-10-02 Rev: v3-A

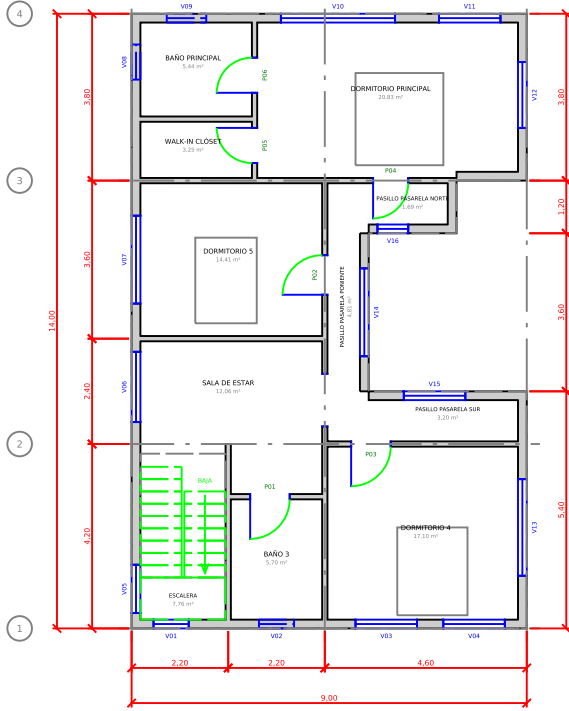

PLANTA SEGUNDO PISO
1:50

NPT +2.85



CUADRO DE SUPERFICIES — Segundo Piso

Ruizinto	A ejes (doc)	GBI (modelo)
Escalera	9.24	7.76
Baño 3	6.60	5.76
Sala de Estar	13.20	12.06
Dormitorio 4	19.32	17.10
Dormitorio 5	15.84	14.41
Pasillo Pasarela Poniente	6.00	4.81
Pasillo Pasarela Sur	4.32	3.20
Pasillo Pasarela Norte	2.40	1.60
Walk-in Closet	3.92	3.25
Baño Principal	6.72	5.44
Dormitorio Principal	23.56	20.83
Suma recintos interiores	111.12	96.24

A: ejes, cancela; doc: al cuadro del documento; rev: G: verificado recibo por recibo.
(GBI): superficie medida del Space del modelo ProCAD; descomenta la huella de muro.
Entonces (cancela, patio, jardín) en sumas.

CUADRO DE VANOS

Cod	Tipo	Ancho x alto	Anteposico	Ostaculo	Apertura (patron de diseño)
P01	Puerta	0.90 x 2.10	0.00	2.10	alre a Baño 3, bisagra der.
P02	Puerta	0.90 x 2.10	0.00	2.10	alre a Dormitorio 5, bisagra izq.
P03	Puerta	0.90 x 2.10	0.00	2.10	alre a Dormitorio 4, bisagra der.
P04	Puerta	0.80 x 2.10	0.00	2.10	alre a Pasillo Pasarela Norte, bisagra der.
P05	Puerta	0.80 x 2.10	0.00	2.10	alre a Walk-in Closet, bisagra der.
P06	Puerta	0.80 x 2.10	0.00	2.10	alre a Baño Principal, bisagra izq.
—	Fijado	1.20 x 2.30	0.00	2.30	
V01	Ventana	0.80 x 1.25	0.95	2.20	
V02	Ventana	0.80 x 0.80	1.40	2.20	
V03	Ventana	1.40 x 1.25	0.95	2.20	
V04	Ventana	1.40 x 1.25	0.95	2.20	
V05	Ventana	1.30 x 1.25	0.95	2.20	
V06	Ventana	1.40 x 1.25	0.95	2.20	
V07	Ventana	2.00 x 1.25	0.95	2.20	
V08	Ventana	0.80 x 0.80	1.40	2.20	
V09	Ventana	0.90 x 0.80	1.40	2.20	
V10	Ventana	2.40 x 1.25	0.95	2.20	
V11	Ventana	2.40 x 1.25	0.95	2.20	
V12	Ventana	1.50 x 1.25	0.95	2.20	
V13	Ventana	2.00 x 1.25	0.95	2.20	
V14	Ventana	2.00 x 2.05	0.15	2.20	
V15	Ventana	1.40 x 2.05	0.15	2.20	
V16	Ventana	0.70 x 2.05	0.15	2.20	

PLANTA SEGUNDO PISO

Vivienda unifamiliar 2 pisos con patio interior — anteproyecto, v3 (reconstruida desde sources/Test)
Escala: 1:50 (A2) — Cortes en metros — NPT +2.85

Fuente: <Shogun/modelluasa_v3_PCH3 (objetos Arch), cortes a +1.20 m
Comuna, no y RUC: por definir (este por)
Norte según el documento rev. G; no hay levantamiento del sitio

Abastecimiento y biogas: patrón de diseño (P1, P2), sin verificación normativa
Sin verificado normativo: umbrales OGC sin transitorio (MCONC/USO)
Fecha: 2020-10-02 Rev: v-3A