


4
3
2
1

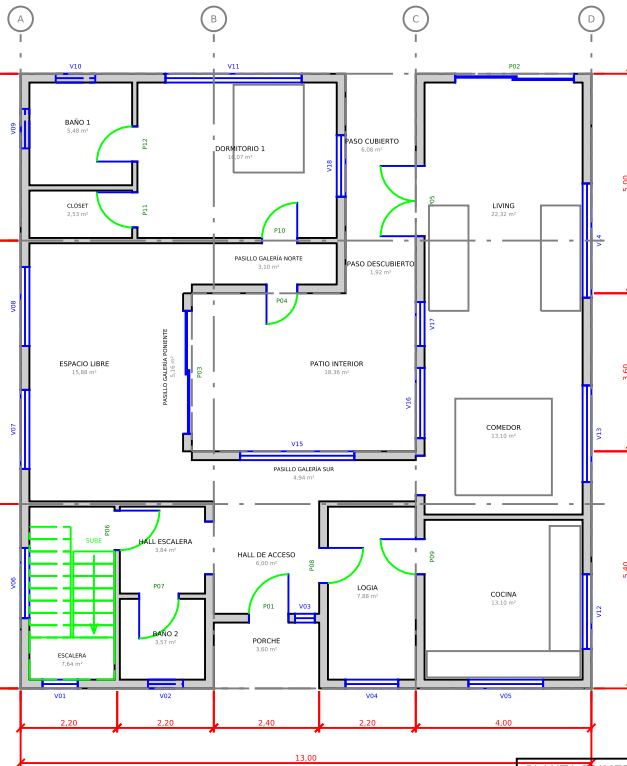

PLANTA PRIMER PISO
1:50



NPT ±0.00

CUADRO DE SUPERFICIES — Primer Piso

Recinto	A (área) (doc)	GBL (modulo)
Escalera	9.24	7.64
Baño 2	4.62	2.57
Hall Escalera	4.62	3.84
Hall de Acceso	6.48	6.00
Logia	9.24	7.68
Porche (ext.)	3.60	3.60
Escalera Libre	17.40	15.98
Pasillo Galería Poniente	6.00	5.16
Pasillo Galería Sur	6.12	4.94
Pasillo Galería Norte	4.20	3.10
Closet	3.12	2.53
Baño 1	6.76	5.40
Dormitorio 1	18.24	16.07
Cocina	15.60	13.10
Comedor	14.80	13.10
Living	22.60	22.32
Patio Interior (ext.)	18.36	18.36
Paso Cubierto (ext.)	6.08	6.08
Paso Descubierta (ext.)	1.92	1.92
Suma recintos interiores	152.04	130.61

A área coincide con el cuadro del documento rev. G (verificado recibo por recinto).
GBL superficie medida del Sapo de mano FreeCAD, decorada la huella de mano.
Exteriores (porche, patio, pasillo no surten).

CUADRO DE VANOS


Cid.	Tipo	Ancho x alto	Antepecho	Dintel	Apertura (patrón de diseño)
P01	Puerta	0.90 x 2.10	-0.00	2.10	alve a Hall de Acceso, logia der.
P02	Puerta	2.10 x 2.35	-0.00	2.35	comedor.
P03	Puerta	2.00 x 2.35	-0.00	2.35	comedor.
P04	Puerta	0.90 x 2.10	-0.00	2.10	alve a Patio interior, logia der.
P05	Puerta	0.90 x 2.10	-0.00	2.10	2 Hall a Paso Cubierta, logia surten
P06	Puerta	0.90 x 2.10	-0.00	2.10	alve a Hall de Acceso, logia der.
P07	Puerta	0.90 x 2.10	-0.00	2.10	alve a Baño 2, logia der.
P08	Puerta	0.90 x 2.10	-0.00	2.10	alve a Logia, logia der.
P09	Puerta	0.90 x 2.10	-0.00	2.10	alve a Logia, logia der.
P10	Puerta	0.90 x 2.10	-0.00	2.10	alve a Dormitorio 1, logia der.
P11	Puerta	0.90 x 2.10	-0.00	2.10	alve a Closet, logia der.
P12	Puerta	0.90 x 2.10	-0.00	2.10	alve a Baño 1, logia der.
-	Paso	2.20 x 2.50	0.00	2.50	
V01	Ventana	0.90 x 2.50	0.00	2.50	
V02	Ventana	0.90 x 2.50	0.00	2.50	
V03	Ventana	0.90 x 2.50	0.00	2.50	
V04	Ventana	0.90 x 2.50	0.00	2.50	
V05	Ventana	0.90 x 2.50	0.00	2.50	
V06	Ventana	0.90 x 2.50	0.00	2.50	
V07	Ventana	0.90 x 2.50	0.00	2.50	
V08	Ventana	0.90 x 2.50	0.00	2.50	
V09	Ventana	0.90 x 2.50	0.00	2.50	
V10	Ventana	0.90 x 2.50	0.00	2.50	
V11	Ventana	0.90 x 2.50	0.00	2.50	
V12	Ventana	0.90 x 2.50	0.00	2.50	
V13	Ventana	0.90 x 2.50	0.00	2.50	
V14	Ventana	0.90 x 2.50	0.00	2.50	
V15	Ventana	0.90 x 2.50	0.00	2.50	
V16	Ventana	0.90 x 2.50	0.00	2.50	
V17	Ventana	0.90 x 2.50	0.00	2.50	
V18	Ventana	0.90 x 2.50	0.00	2.50	

PLANTA PRIMER PISO

Vivienda unifamiliar 2 pisos con patio interior — anteproyecto, v2 (reconstruida desde rev. Gm)
Escala: 1:50 (A2) — Cotas en metros — NPT ±0.00

Fuente: <2>planos, v2 (2023) (datos Archi, cortes a ±1.20 m)
Comuna, no y PRC por definir (este plano)
Norte según el documento rev. G, no hay levantamiento del sitio

Abstracción y biografía: patrón de diseño (P2, P8), sin verificación normativa
Sin verificación normativa: umbrales OGUC sin transitorio (INCORUGOS)
Fecha: 2023-10-01 — Rev. v2-A

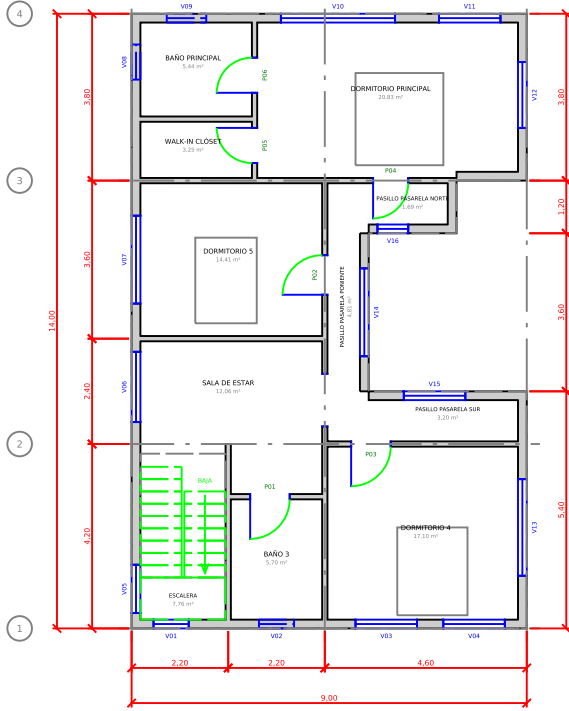

PLANTA SEGUNDO PISO
1:50

NPT +2.85



CUADRO DE SUPERFICIES — Segundo Piso

Recinto	A ejes (doc)	GBI (modelo)
Escalera	9.24	7.76
Baño 3	6.60	5.76
Sala de Estar	13.20	12.06
Dormitorio 4	19.32	17.10
Dormitorio 5	15.84	14.41
Pasillo Pasarela Poniente	6.00	4.81
Pasillo Pasarela Sur	4.32	3.20
Pasillo Pasarela Norte	2.40	1.60
Walk-in Closet	3.92	3.25
Baño Principal	6.72	5.44
Dormitorio Principal	23.56	20.83
Suma recintos interiores	111.12	96.24

A: ejes, cancela; doc: al cuadro del documento; rev: G: verificado recibo por recibí.
GBI: superficie medida del Space del modelo ProCAD; decorada la huella de muro.
Enteros (cancela, patio, pajar) en sumas.

CUADRO DE VANOS

Cod	Tipo	Ancho x alto	Antepecho	Orient	Apertura (patrón de diseño)
P01	Puerta	0.90 x 2.10	0.00	2.10	alre a Baño 3, bisagra der.
P02	Puerta	0.90 x 2.10	0.00	2.10	alre a Dormitorio 5, bisagra izq.
P03	Puerta	0.90 x 2.10	0.00	2.10	alre a Dormitorio 4, bisagra der.
P04	Puerta	0.80 x 2.10	0.00	2.10	alre a Pasillo Pasarela Norte, bisagra der.
P05	Puerta	0.80 x 2.10	0.00	2.10	alre a Walk-in Closet, bisagra der.
P06	Puerta	0.80 x 2.10	0.00	2.10	alre a Baño Principal, bisagra izq.
—	Flojo	1.20 x 2.30	0.00	2.30	
V01	Ventana	0.80 x 1.25	0.95	2.20	
V02	Ventana	0.80 x 0.80	1.40	2.20	
V03	Ventana	1.40 x 1.25	0.95	2.20	
V04	Ventana	1.40 x 1.25	0.95	2.20	
V05	Ventana	1.30 x 1.25	0.95	2.20	
V06	Ventana	1.40 x 1.25	0.95	2.20	
V07	Ventana	2.00 x 1.25	0.95	2.20	
V08	Ventana	0.80 x 0.80	1.40	2.20	
V09	Ventana	0.90 x 0.80	1.40	2.20	
V10	Ventana	2.40 x 1.25	0.95	2.20	
V11	Ventana	2.40 x 1.25	0.95	2.20	
V12	Ventana	1.50 x 1.25	0.95	2.20	
V13	Ventana	2.20 x 1.25	0.95	2.20	
V14	Ventana	2.00 x 2.05	0.15	2.20	
V15	Ventana	1.40 x 2.05	0.15	2.20	
V16	Ventana	0.70 x 2.05	0.15	2.20	

PLANTA SEGUNDO PISO

Vivienda unifamiliar 2 pisos con patio interior — anteproyecto, v2 (reconstruida desde rev. GH)
Escala: 1:50 (A2) — Cotas en metros — NPT: +2.85

Fuente: v2planeta/cuadros2PCSD (objetos Archi), cortes a +1.20 m
Comuna, rol y RUC: por definir (este plano)
Norte según el documento rev. G; no hay levantamiento del sitio

Abastecimiento y biogas: patrón de diseño (PL-RE), sin verificación normativa
Sin verificado normativo: umbrales OGC sin transitorio (MCONC/USO)
Fecha: 2020-10-01 Rev: v-A