

4

3

2

1

A

B

C

D



CUADRO DE SUPERFICIES — Primer Piso

Recinto	A (pies (dec))	GB (metros)
Escalera	9.24	7.84
Baño 2	4.62	3.57
Hall Escalera	4.62	3.94
Hall de Acceso	6.48	6.00
Logia	9.24	7.88
Pierche (ext.)	3.60	3.60
Espacio Libre	17.40	16.88
Paseo Galería Poniente	6.00	5.16
Paseo Galería Sur	6.12	4.94
Paseo Galería Norte	4.20	3.10
Closet	3.12	2.53
Baño 1	6.76	5.45
Dormitorio 1	18.24	18.07
Cocina	15.60	13.10
Comedor	14.80	13.10
Living	20.60	22.32
Patio Interior (ext.)	18.36	16.36
Paseo Cubierto (ext.)	6.00	6.00
Paseo Descubierto (ext.)	1.80	1.80
Suma recintos interiores	192.04	136.61

A área coincide con el cuadro del documento rev. G (verificado recibo por metro).
GB: superficie medida del espacio del modelo FreeCAD, despreciable la falta de decimales.
Excepciones (puerco, patio, pasillo no se suman).

CUADRO DE VANOS

Cod.	Tipo	Ancho x alto	Anteproyecto	Diferal	Apertura (quitrón de diseño)
P01	Puerta	0.80 x 2.10	0.00	2.10	área x Hall de Acceso, Integrar área
P02	Puerta	2.70 x 2.30	0.00	2.30	cuerpo de
P03	Puerta	2.00 x 1.20	0.00	2.30	cuerpo de
P04	Puerta	0.70 x 2.10	0.00	2.10	área x Hall de Acceso, Integrar área
P05	Puerta	0.80 x 2.30	0.00	2.30	área x Hall de Acceso, Integrar área
P06	Puerta	0.80 x 2.10	0.00	2.10	área x Hall de Acceso, Integrar área
P07	Puerta	0.80 x 2.10	0.00	2.10	área x Hall de Acceso, Integrar área
P08	Puerta	0.80 x 2.10	0.00	2.10	área x Hall de Acceso, Integrar área
P09	Puerta	0.80 x 2.10	0.00	2.10	área x Hall de Acceso, Integrar área
P10	Puerta	0.80 x 2.10	0.00	2.10	área x Hall de Acceso, Integrar área
P11	Puerta	0.80 x 2.10	0.00	2.10	área x Hall de Acceso, Integrar área
P12	Puerta	0.80 x 2.10	0.00	2.10	área x Hall de Acceso, Integrar área
—	Paseo	1.20 x 2.30	0.00	2.30	área x Hall de Acceso, Integrar área
—	Paseo	0.80 x 2.30	0.00	2.30	área x Hall de Acceso, Integrar área
V01	Ventana	0.80 x 1.20	0.86	2.30	área x Hall de Acceso, Integrar área
V02	Ventana	0.80 x 0.80	1.40	2.30	área x Hall de Acceso, Integrar área
V03	Ventana	0.80 x 1.20	0.86	2.30	área x Hall de Acceso, Integrar área
V04	Ventana	1.20 x 1.20	0.86	2.30	área x Hall de Acceso, Integrar área
V05	Ventana	1.70 x 1.10	1.10	2.30	área x Hall de Acceso, Integrar área
V06	Ventana	1.80 x 1.20	0.86	2.30	área x Hall de Acceso, Integrar área
V07	Ventana	1.80 x 1.20	0.86	2.30	área x Hall de Acceso, Integrar área
V08	Ventana	1.80 x 1.20	0.86	2.30	área x Hall de Acceso, Integrar área
V09	Ventana	1.80 x 1.20	0.86	2.30	área x Hall de Acceso, Integrar área
V10	Ventana	0.80 x 0.80	1.40	2.30	área x Hall de Acceso, Integrar área
V11	Ventana	0.80 x 1.20	0.86	2.30	área x Hall de Acceso, Integrar área
V12	Ventana	1.70 x 1.10	1.10	2.30	área x Hall de Acceso, Integrar área
V13	Ventana	2.10 x 1.80	0.86	2.30	área x Hall de Acceso, Integrar área
V14	Ventana	2.80 x 2.30	0.15	2.35	área x Hall de Acceso, Integrar área
V15	Ventana	1.80 x 1.20	0.15	2.35	área x Hall de Acceso, Integrar área
V16	Ventana	1.80 x 1.20	0.15	2.35	área x Hall de Acceso, Integrar área
V17	Ventana	1.00 x 1.20	0.15	2.35	área x Hall de Acceso, Integrar área
V18	Ventana	1.40 x 1.25	0.86	2.30	área x Hall de Acceso, Integrar área

PLANTA PRIMER PISO

Vivienda unifamiliar 2 pisos con patio interior — anteproyecto, v2 (reconstruido desde rev. G11)
Escala: 1:50 (4/2) — Cortes en metros — NPT #0.00


Fuente: [c3d/area/area_v2_PDFM](#) (álgebra Area), cortes a +1.20 m
Comenzó en el PRC por defecto (área plana)
Nota según el documento rev. G: no hay levantamiento del sitio

Abastecimiento y drenaje: patio de diseño (R1, R2), sin verificación normativa
Sin verificación normativa: unidades OSBC sin transitorio (NOMEX-ISO)
Fecha: 2025-10-01 — Rev. 42-A

PLANTA PRIMER PISO

1:50



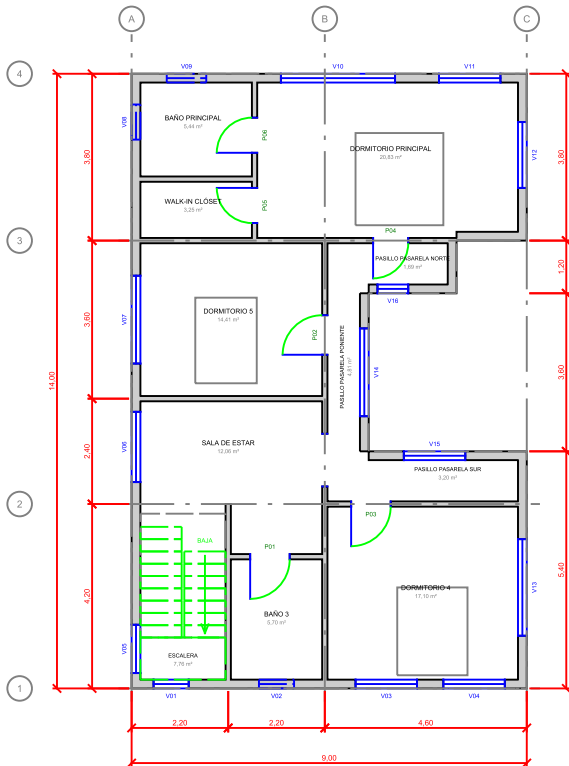

PLANTA SEGUNDO PISO
1:50



CUADRO DE SUPERFICIES — Segundo Piso

Recinto	A área (m²)	GB (m²)
Escalera	9.24	7.76
Baño 3	6.60	5.70
Sala de Estar	13.20	12.00
Dormitorio 4	19.32	17.10
Dormitorio S	16.84	14.41
Paseo Pasarela Poniente	6.00	4.91
Paseo Pasarela Sur	4.32	3.20
Paseo Pasarela Norte	2.40	1.69
Walk-in Closet	3.92	3.25
Baño Principal	6.72	5.44
Dormitorio Principal	23.56	20.83
Suma recinto interior	111.12	96.24

A área construida según el cuadro del documento rev. G (verificado, modificado por modificado).
GB: superficie construida del Sistema del modelo (ProCAD), documentada la fuente de datos.
Exteriores (patio, jardín, terraza, etc.) no están.

CUADRO DE VANOS

Cód.	Tipo	Ancho x alto	Anteproyecto	Costal	Apertura (patio de diseño)
V01	Puerta	0.80 x 2.10	0.00	2.10	aire a Baño 3, pasaje del
V02	Puerta	0.80 x 2.10	0.00	2.10	aire a Dormitorio S, pasaje del
V03	Puerta	0.80 x 2.10	0.00	2.10	aire a Dormitorio S, pasaje del
V04	Puerta	0.80 x 2.10	0.00	2.10	aire a Paseo Pasarela Norte, pasaje del
V05	Puerta	0.80 x 2.10	0.00	2.10	aire a Walk-in Closet, pasaje del
V06	Puerta	0.80 x 2.10	0.00	2.10	aire a Baño Principal, pasaje del
V07	Puerta	0.80 x 2.10	0.00	2.10	
V08	Puerta	0.80 x 2.10	0.00	2.10	
V09	Ventana	0.80 x 1.20	0.85	2.20	
V10	Ventana	0.80 x 1.20	1.40	2.20	
V11	Ventana	1.40 x 1.20	0.95	2.20	
V12	Ventana	1.40 x 1.20	0.95	2.20	
V13	Ventana	1.10 x 1.20	0.95	2.20	
V14	Ventana	0.80 x 1.20	0.95	2.20	
V15	Ventana	2.00 x 1.20	0.85	2.20	
V16	Ventana	0.80 x 0.80	1.40	2.20	
V17	Ventana	0.80 x 0.80	1.40	2.20	
V18	Ventana	2.00 x 1.20	0.95	2.20	
V19	Ventana	2.00 x 1.20	0.95	2.20	
V20	Ventana	1.40 x 1.20	0.95	2.20	
V21	Ventana	1.10 x 1.20	0.95	2.20	
V22	Ventana	2.00 x 2.00	0.15	2.20	
V23	Ventana	2.00 x 2.00	0.15	2.20	
V24	Ventana	0.70 x 2.05	0.15	2.20	

PLANTA SEGUNDO PISO

Ventana unifamiliar 2 pisos con patio interior — anteproyecto, v2 (reconstruida desde rev. G14)
Escala: 1:50 (A2) Cotas en metros: NPT +2.85

Fuente: c:\diseños\area_v2\PCDM (álgebra A2), cotas a +1.20 m
Comenzó: nro y PRC por diseño (álgebra)
Nota según el documento: G no hay levantamiento del sitio

Abstracción y limpieza: patios de diseño (R1, R2), sin verificación normativa
Sin verificación normativa: unidades OSUC sin transitorio (NOCON/LISO)
Fecha: 2025-10-01 - Rev. 42-A