



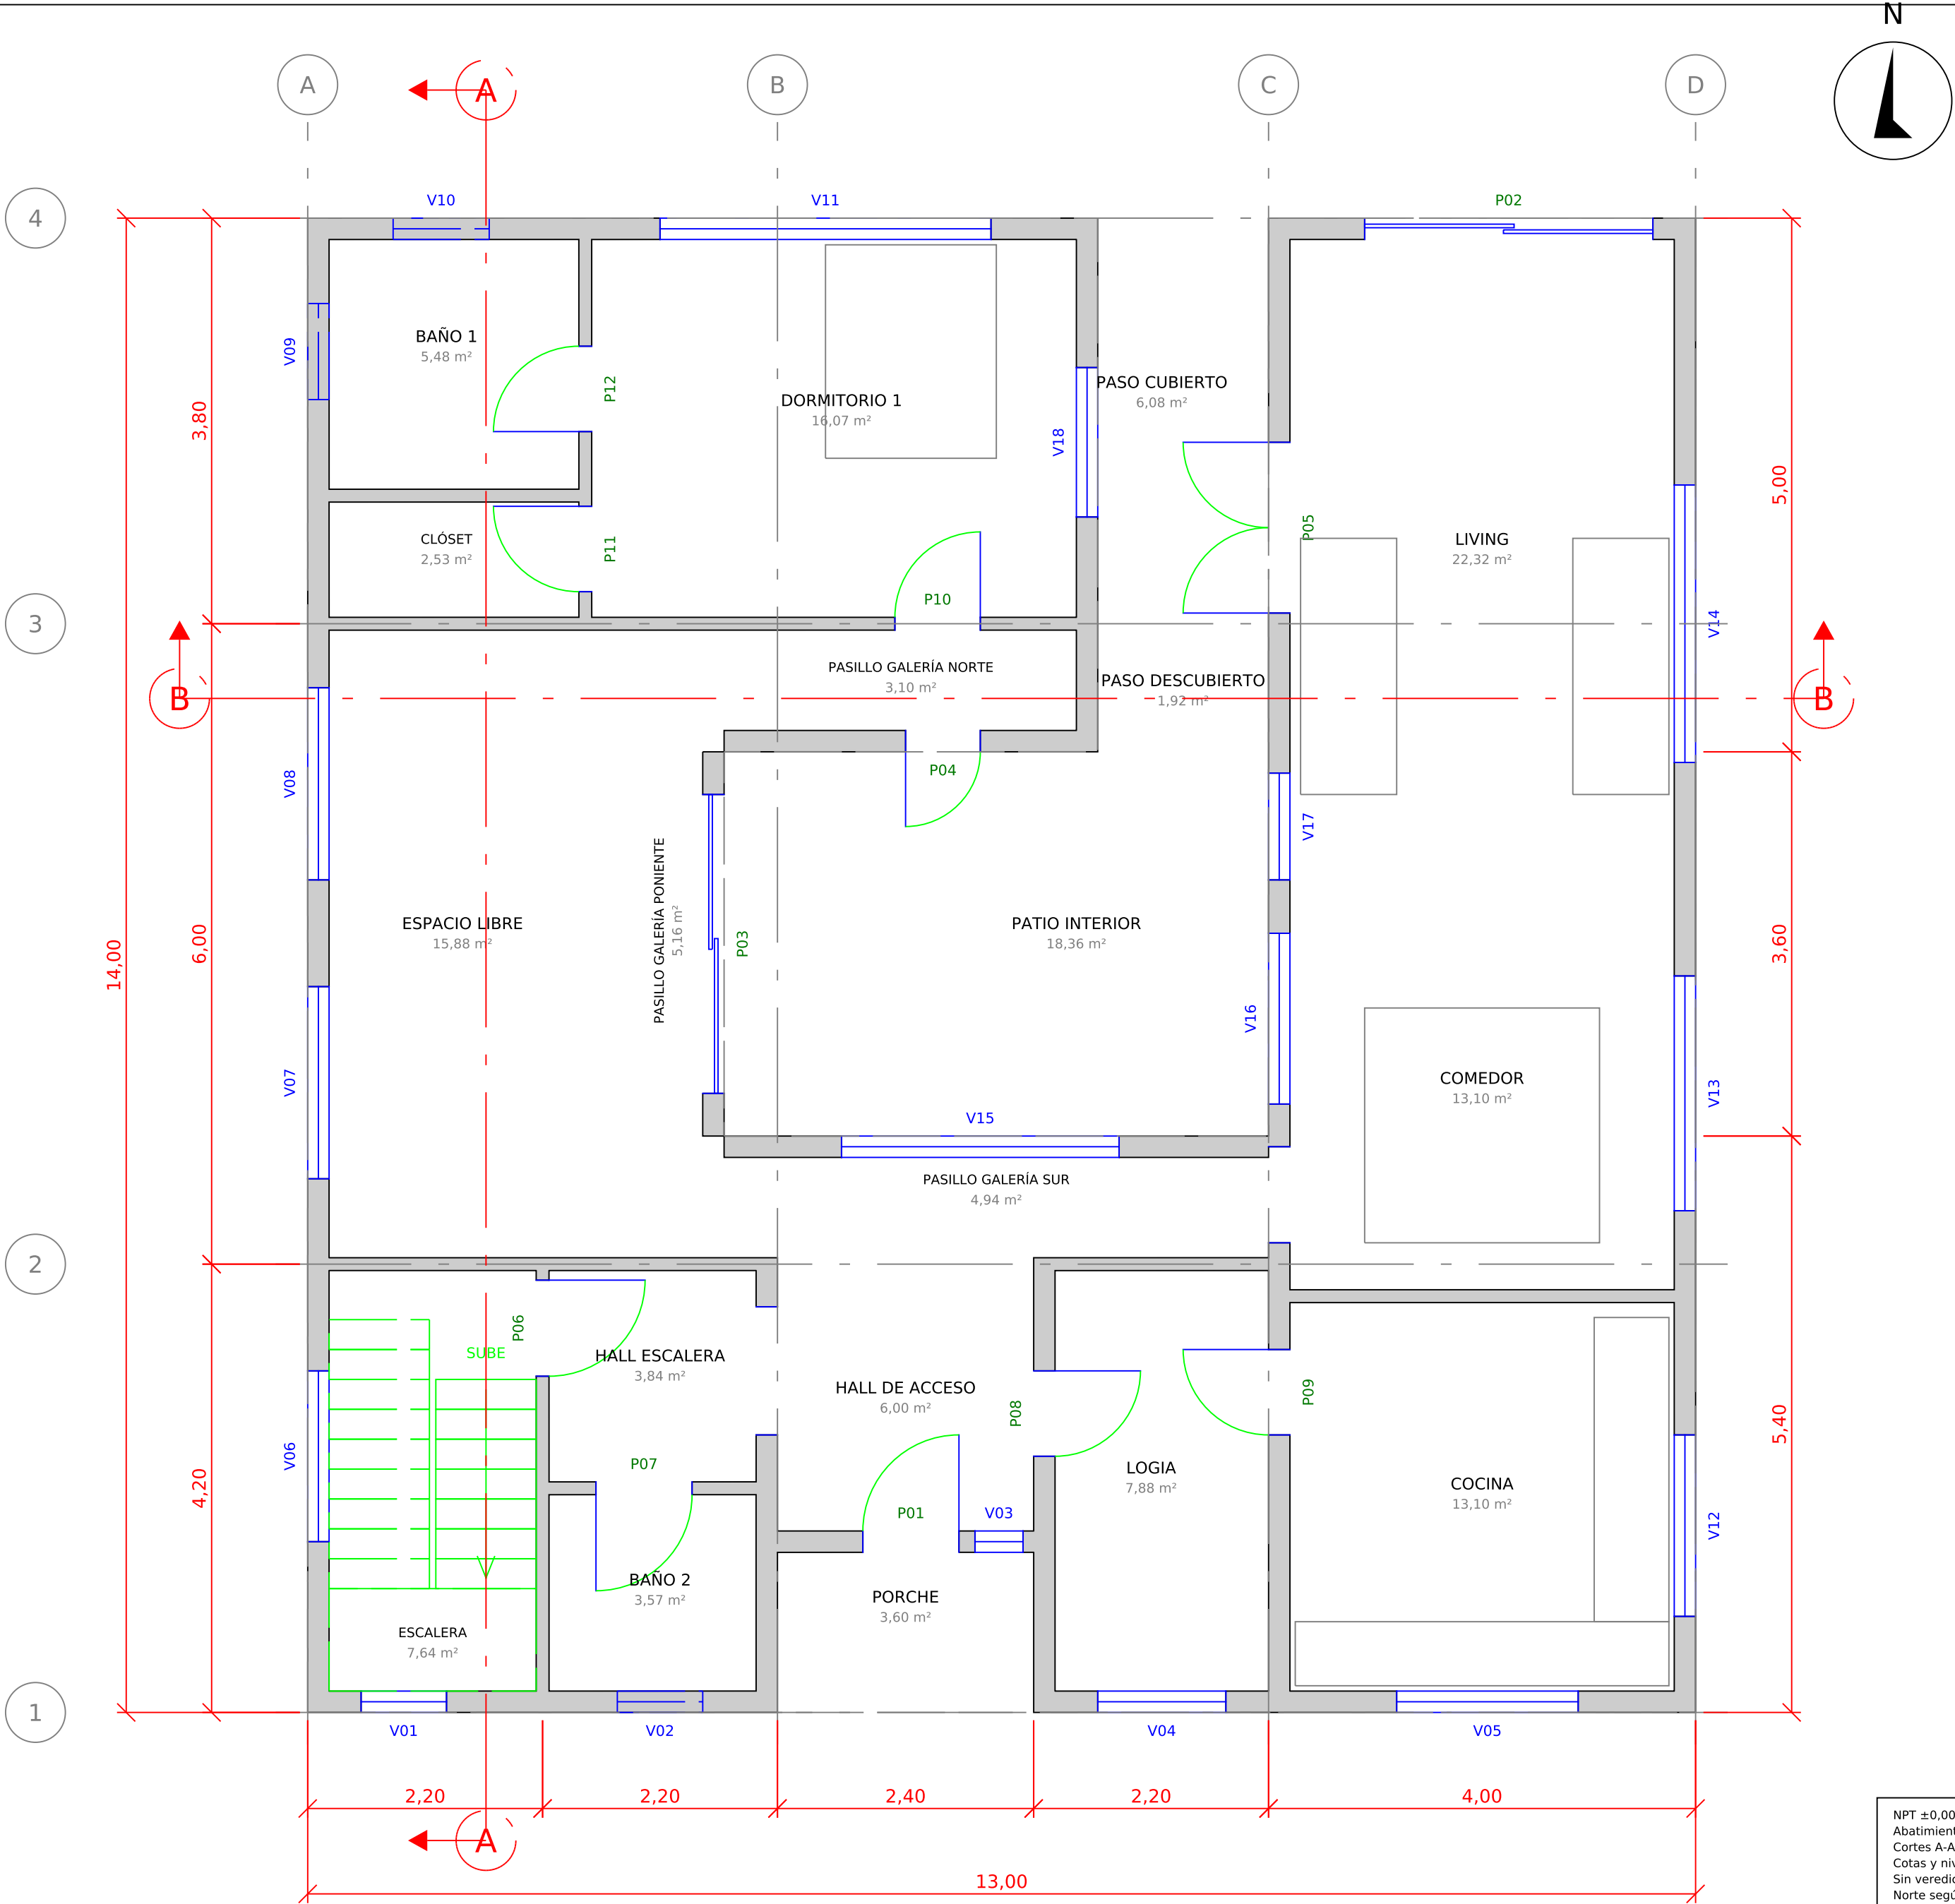

PLANTA PRIMER PISO

1:50

NPT ±0,00

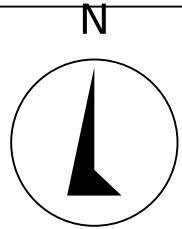

CUADRO DE SUPERFICIES — Primer Piso

| Recinto                  | A ejes (doc) | Útil (modelo) |
|--------------------------|--------------|---------------|
| Escalera                 | 9,24         | 7,64          |
| Baño 2                   | 4,62         | 3,57          |
| Hall Escalera            | 4,62         | 3,84          |
| Hall de Acceso           | 6,48         | 6,00          |
| Logia                    | 9,24         | 7,88          |
| Porche (ext.)            | 3,60         | 3,60          |
| Espacio Libre            | 17,40        | 15,88         |
| Pasillo Galería Poniente | 6,00         | 5,16          |
| Pasillo Galería Sur      | 6,12         | 4,94          |
| Pasillo Galería Norte    | 4,20         | 3,10          |
| Clóset                   | 3,12         | 2,53          |
| Baño 1                   | 6,76         | 5,48          |
| Dormitorio 1             | 18,24        | 16,07         |
| Cocina                   | 15,60        | 13,10         |
| Comedor                  | 14,80        | 13,10         |
| Living                   | 25,60        | 22,32         |
| Patio Interior (ext.)    | 18,36        | 18,36         |
| Paso Cubierto (ext.)     | 6,08         | 6,08          |
| Paso Descubierta (ext.)  | 1,92         | 1,92          |
| Suma recintos interiores | 152,04       | 130,61        |

A ejes: coincide con el cuadro del documento rev. G (verificado recinto por recinto).  
Útil: superficie medida del Space del modelo FreeCAD, descontada la huella de muros.  
Exteriores (porche, patios, paso) no suman.

CUADRO DE VANOS


| Cód. | Tipo    | Ancho x alto | Antepecho | Dintel | Apertura (patrón de diseño)            |
|------|---------|--------------|-----------|--------|----------------------------------------|
| P01  | Puerta  | 0,90 x 2,10  | -0,00     | 2,10   | abre a Hall de Acceso, bisagra der.    |
| P02  | Puerta  | 2,70 x 2,36  | -0,00     | 2,36   | corredera                              |
| P03  | Puerta  | 2,80 x 2,35  | -0,00     | 2,35   | corredera                              |
| P04  | Puerta  | 0,70 x 2,10  | -0,00     | 2,10   | abre a Patio Interior, bisagra der.    |
| P05  | Puerta  | 1,60 x 2,35  | -0,00     | 2,35   | 2 hojas a Paso Cubierto, bisagra ambos |
| P06  | Puerta  | 0,90 x 2,10  | -0,00     | 2,10   | abre a Hall Escalera, bisagra izq.     |
| P07  | Puerta  | 0,90 x 2,10  | -0,00     | 2,10   | abre a Baño 2, bisagra der.            |
| P08  | Puerta  | 0,80 x 2,10  | -0,00     | 2,10   | abre a Logia, bisagra izq.             |
| P09  | Puerta  | 0,80 x 2,10  | -0,00     | 2,10   | abre a Logia, bisagra der.             |
| P10  | Puerta  | 0,80 x 2,10  | -0,00     | 2,10   | abre a Dormitorio 1, bisagra der.      |
| P11  | Puerta  | 0,80 x 2,10  | -0,00     | 2,10   | abre a Clóset, bisagra der.            |
| P12  | Puerta  | 0,80 x 2,10  | -0,00     | 2,10   | abre a Baño 1, bisagra izq.            |
| —    | Paso    | 1,20 x 2,30  | 0,00      | 2,30   |                                        |
| —    | Paso    | 0,90 x 2,30  | 0,00      | 2,30   |                                        |
| V01  | Ventana | 0,80 x 1,25  | 0,95      | 2,20   |                                        |
| V02  | Ventana | 0,80 x 0,80  | 1,40      | 2,20   |                                        |
| V03  | Ventana | 0,45 x 1,35  | 0,95      | 2,30   |                                        |
| V04  | Ventana | 1,20 x 1,25  | 0,95      | 2,20   |                                        |
| V05  | Ventana | 1,70 x 1,10  | 1,10      | 2,20   |                                        |
| V06  | Ventana | 1,60 x 1,35  | 0,95      | 2,30   |                                        |
| V07  | Ventana | 1,80 x 1,25  | 0,95      | 2,20   |                                        |
| V08  | Ventana | 1,80 x 1,25  | 0,95      | 2,20   |                                        |
| V09  | Ventana | 0,90 x 0,80  | 1,40      | 2,20   |                                        |
| V10  | Ventana | 0,90 x 0,80  | 1,40      | 2,20   |                                        |
| V11  | Ventana | 3,10 x 1,25  | 0,95      | 2,20   |                                        |
| V12  | Ventana | 1,70 x 1,10  | 1,10      | 2,20   |                                        |
| V13  | Ventana | 2,20 x 1,80  | 0,55      | 2,35   |                                        |
| V14  | Ventana | 2,60 x 2,20  | 0,15      | 2,35   |                                        |
| V15  | Ventana | 2,60 x 2,20  | 0,15      | 2,35   |                                        |
| V16  | Ventana | 1,60 x 2,20  | 0,15      | 2,35   |                                        |
| V17  | Ventana | 1,00 x 2,20  | 0,15      | 2,35   |                                        |
| V18  | Ventana | 1,40 x 1,25  | 0,95      | 2,20   |                                        |

NPT ±0,00. Fuente: exports/model/casa\_v4.FCStd, corte a +1,20 m.  
Abatimiento y bisagras: patrón de diseño (R1-R9), sin verificación normativa.  
Cortes A-A y B-B: lámina CORTES.  
Cotas y niveles en metros. NPT ±0,00.  
Sin veredicto normativo: umbrales OGUC sin transcribir (INCONCLUSO).  
Norte según el documento rev. G; no hay levantamiento del sitio.


PLANTA PRIMER PISO

Vivienda unifamiliar 2 pisos con patio interior — anteproyecto, versión v4  
Propietario: por definir  
Arquitecto: por definir Registro: por definir  
Dirección: por definir  
Rol: por definir · Comuna: por definir

Escala 1:50  
Papel A2 (594 x 420 mm)  
Fecha 2026-10-04 Rev. v4-A  
LÁMINA  
1 / 5

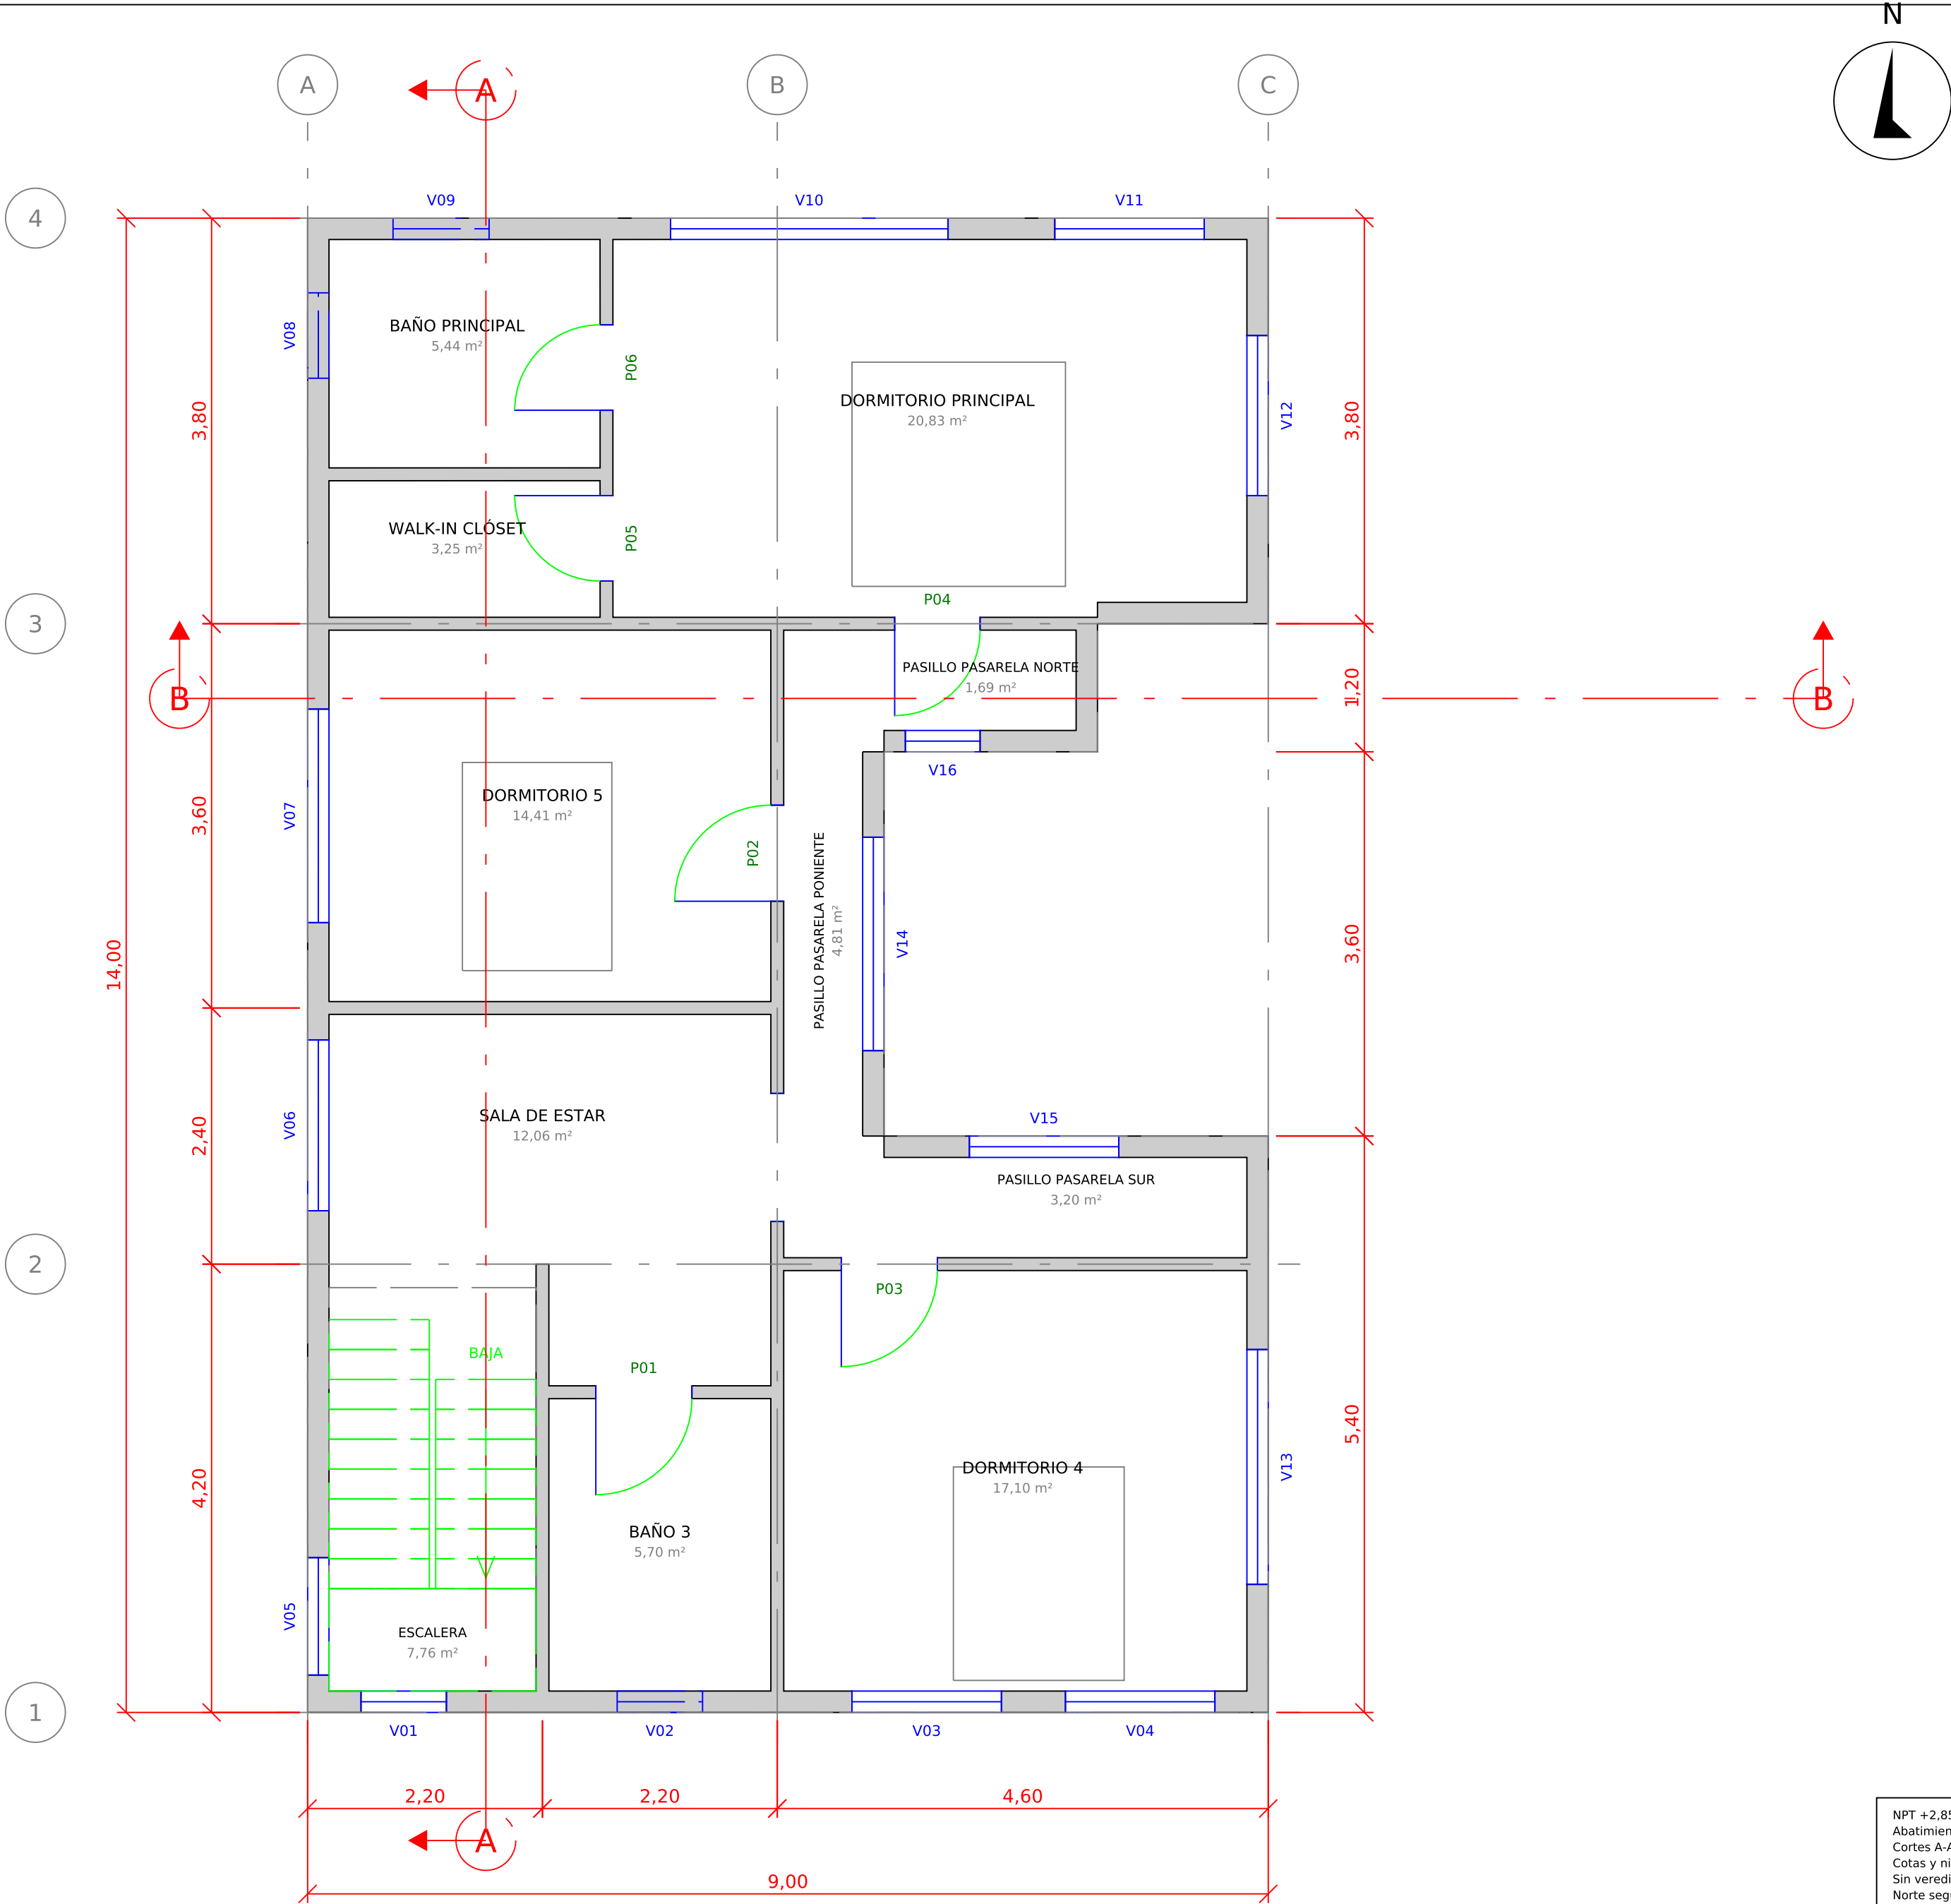

PLANTA SEGUNDO PISO  
1:50

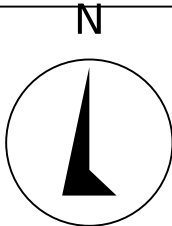

CUADRO DE SUPERFICIES — Segundo Piso

| Recinto                   | A ejes (doc) | Útil (modelo) |
|---------------------------|--------------|---------------|
| Escalera                  | 9,24         | 7,76          |
| Baño 3                    | 6,60         | 5,70          |
| Sala de Estar             | 13,20        | 12,06         |
| Dormitorio 4              | 19,32        | 17,10         |
| Dormitorio 5              | 15,84        | 14,41         |
| Pasillo Pasarela Poniente | 6,00         | 4,81          |
| Pasillo Pasarela Sur      | 4,32         | 3,20          |
| Pasillo Pasarela Norte    | 2,40         | 1,69          |
| Walk-in Clóset            | 3,92         | 3,25          |
| Baño Principal            | 6,72         | 5,44          |
| Dormitorio Principal      | 23,56        | 20,83         |
| Suma recintos interiores  | 111,12       | 96,24         |

A ejes: coincide con el cuadro del documento rev. G (verificado recinto por recinto).  
Útil: superficie medida del Space del modelo FreeCAD, descontada la huella de muros.  
Exteriores (porche, patios, paso) no suman.

CUADRO DE VANOS



| Cód. | Tipo    | Ancho x alto | Antepecho | Dintel | Apertura (patrón de diseño)                 |
|------|---------|--------------|-----------|--------|---------------------------------------------|
| P01  | Puerta  | 0,90 x 2,10  | 0,00      | 2,10   | abre a Baño 3, bisagra der.                 |
| P02  | Puerta  | 0,90 x 2,10  | 0,00      | 2,10   | abre a Dormitorio 5, bisagra izq.           |
| P03  | Puerta  | 0,90 x 2,10  | 0,00      | 2,10   | abre a Dormitorio 4, bisagra der.           |
| P04  | Puerta  | 0,80 x 2,10  | 0,00      | 2,10   | abre a Pasillo Pasarela Norte, bisagra der. |
| P05  | Puerta  | 0,80 x 2,10  | 0,00      | 2,10   | abre a Walk-in Clóset, bisagra der.         |
| P06  | Puerta  | 0,80 x 2,10  | 0,00      | 2,10   | abre a Baño Principal, bisagra izq.         |
| —    | Paso    | 1,20 x 2,30  | 0,00      | 2,30   |                                             |
| V01  | Ventana | 0,80 x 1,25  | 0,95      | 2,20   |                                             |
| V02  | Ventana | 0,80 x 0,80  | 1,40      | 2,20   |                                             |
| V03  | Ventana | 1,40 x 1,25  | 0,95      | 2,20   |                                             |
| V04  | Ventana | 1,40 x 1,25  | 0,95      | 2,20   |                                             |
| V05  | Ventana | 1,10 x 1,25  | 0,95      | 2,20   |                                             |
| V06  | Ventana | 1,60 x 1,25  | 0,95      | 2,20   |                                             |
| V07  | Ventana | 2,00 x 1,25  | 0,95      | 2,20   |                                             |
| V08  | Ventana | 0,80 x 0,80  | 1,40      | 2,20   |                                             |
| V09  | Ventana | 0,90 x 0,80  | 1,40      | 2,20   |                                             |
| V10  | Ventana | 2,60 x 1,25  | 0,95      | 2,20   |                                             |
| V11  | Ventana | 1,40 x 1,25  | 0,95      | 2,20   |                                             |
| V12  | Ventana | 1,50 x 1,25  | 0,95      | 2,20   |                                             |
| V13  | Ventana | 2,20 x 1,25  | 0,95      | 2,20   |                                             |
| V14  | Ventana | 2,00 x 2,05  | 0,15      | 2,20   |                                             |
| V15  | Ventana | 1,40 x 2,05  | 0,15      | 2,20   |                                             |
| V16  | Ventana | 0,70 x 2,05  | 0,15      | 2,20   |                                             |

NPT +2.85. Fuente: exports/model/casa\_v4.FCStd, corte a +1,20 m.  
Abatimiento y bisagras: patrón de diseño (R1-R9), sin verificación normativa.  
Cortes A-A y B-B: lámina CORTES.  
Cotas y niveles en metros. NPT ±0,00.  
Sin veredicto normativo: umbrales OGUC sin transcribir (INCONCLUSO).  
Norte según el documento rev. G; no hay levantamiento del sitio.

PLANTA SEGUNDO PISO

Vivienda unifamiliar 2 pisos con patio interior — anteproyecto, versión v4  
Propietario: por definir  
Arquitecto: por definir Registro: por definir  
Dirección: por definir  
Rol: por definir · Comuna: por definir

Escala 1:50  
Papel A2 (594 x 420 mm)  
Fecha 2026-10-04 Rev. v4-A  
LÁMINA  
2 / 5

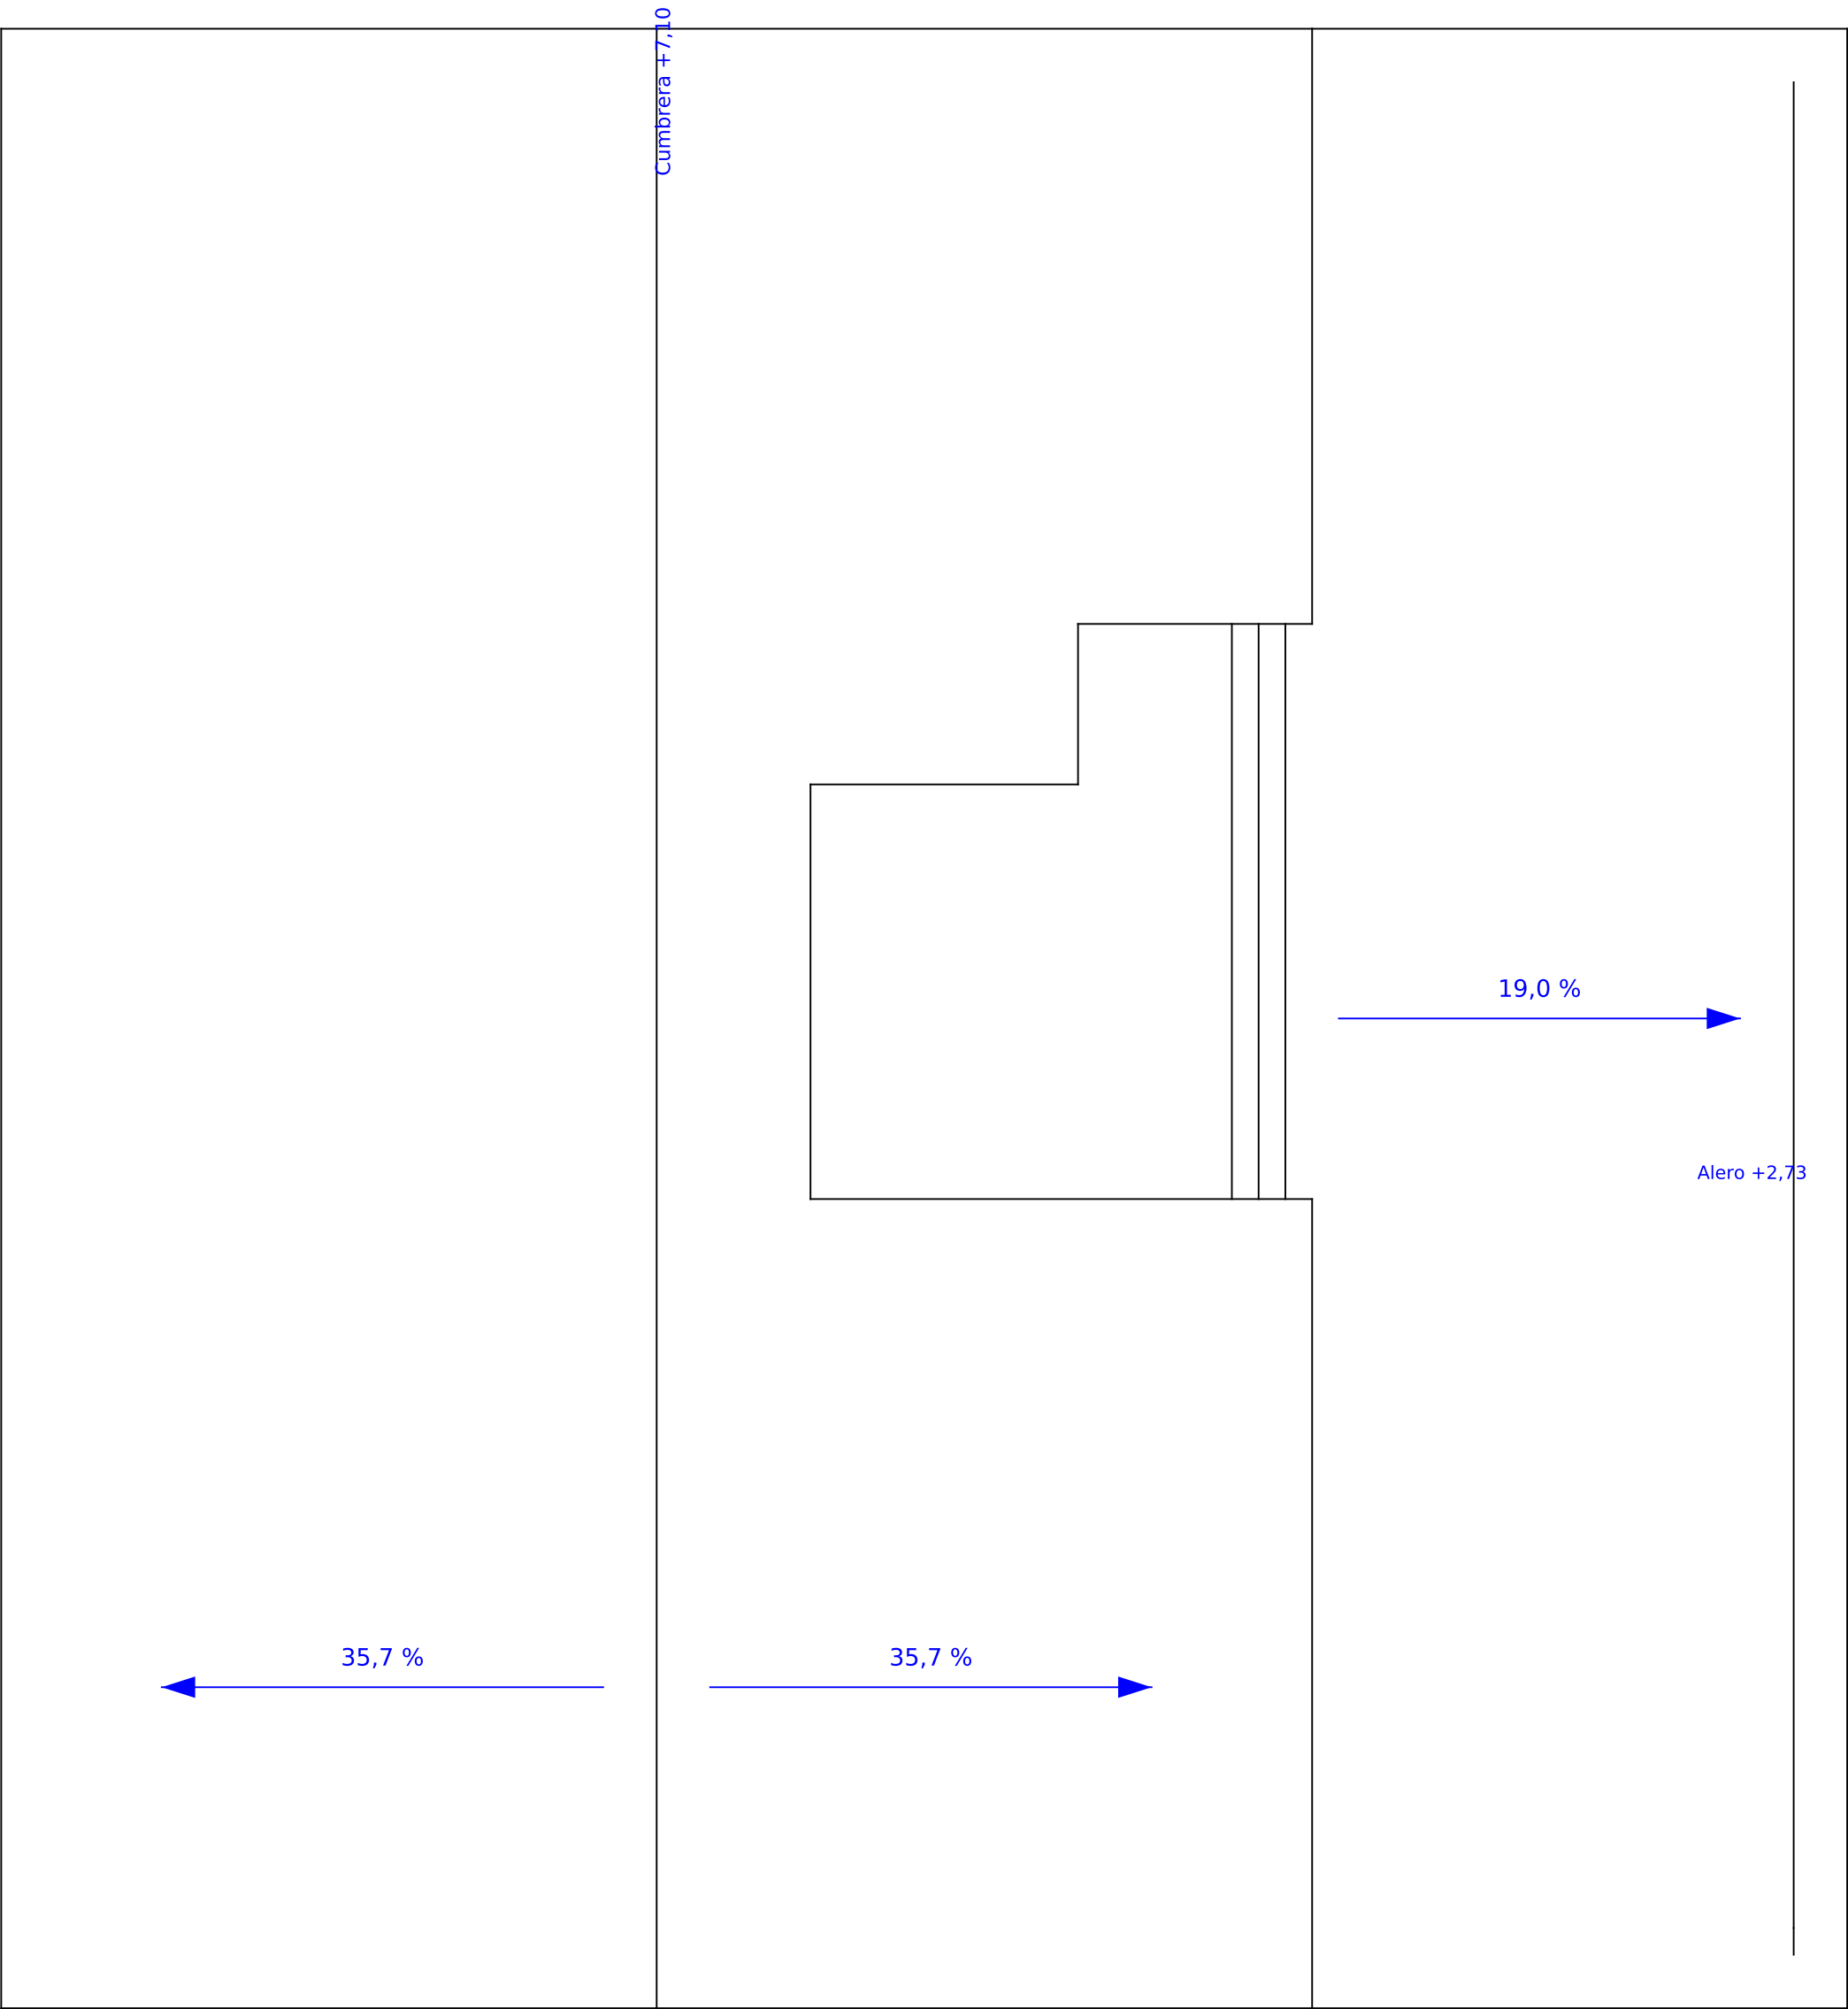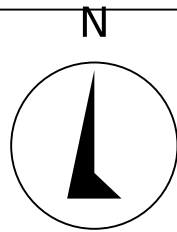

PLANTA DE CUBIERTA

Escala 1:50

Líneas proyectadas del modelo FreeCAD (vista superior, sin líneas ocultas).  
Flechas: sentido de escurrimiento; pendiente calculada de cumbrera y alero.  
Canales y bajadas: no están en el modelo; no se dibujan.  
Cotas y niveles en metros. NPT  $\pm 0,00$ .  
Sin veredicto normativo: umbrales OGUC sin transcribir (INCONCLUSO).  
Norte según el documento rev. G; no hay levantamiento del sitio.

PLANTA DE CUBIERTA

Vivienda unifamiliar 2 pisos con patio interior — anteproyecto, versión v4  
Propietario: por definir  
Arquitecto: por definir    Registro: por definir  
Dirección: por definir  
Rol: por definir    ·    Comuna: por definir


Escala 1:50  
Papel A2 (594 x 420 mm)  
Fecha 2026-10-04    Rev. v4-A

LÁMINA




### ELEVACIÓN SUR

Escala 1:100

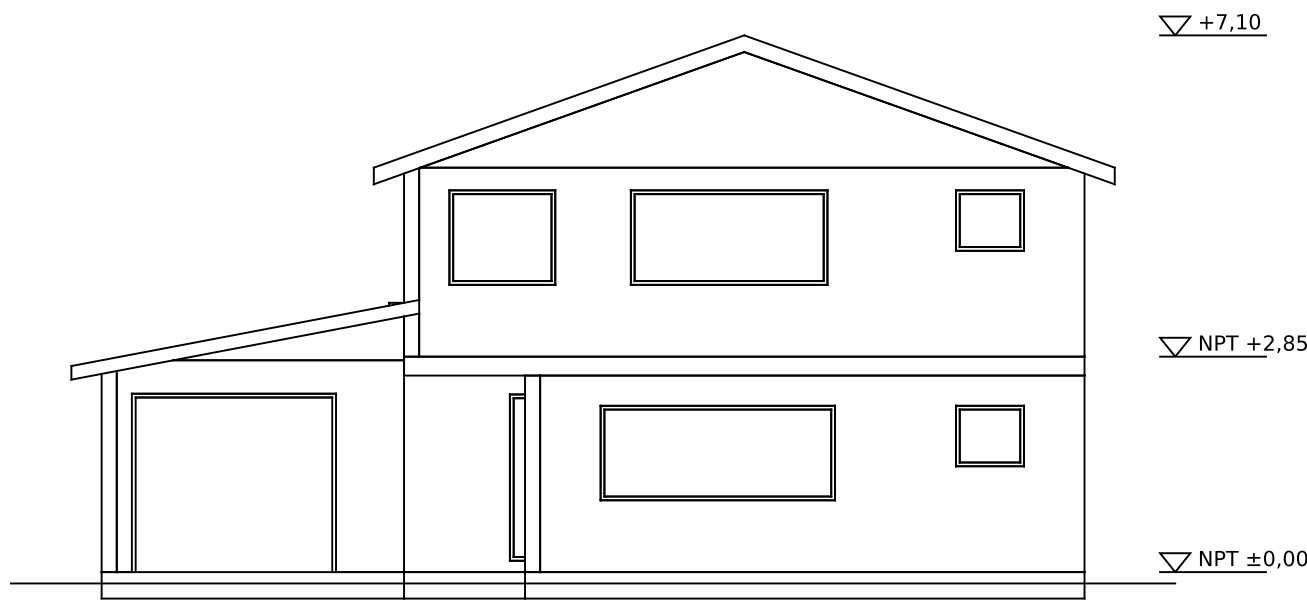


### ELEVACIÓN NORTE

Escala 1:100

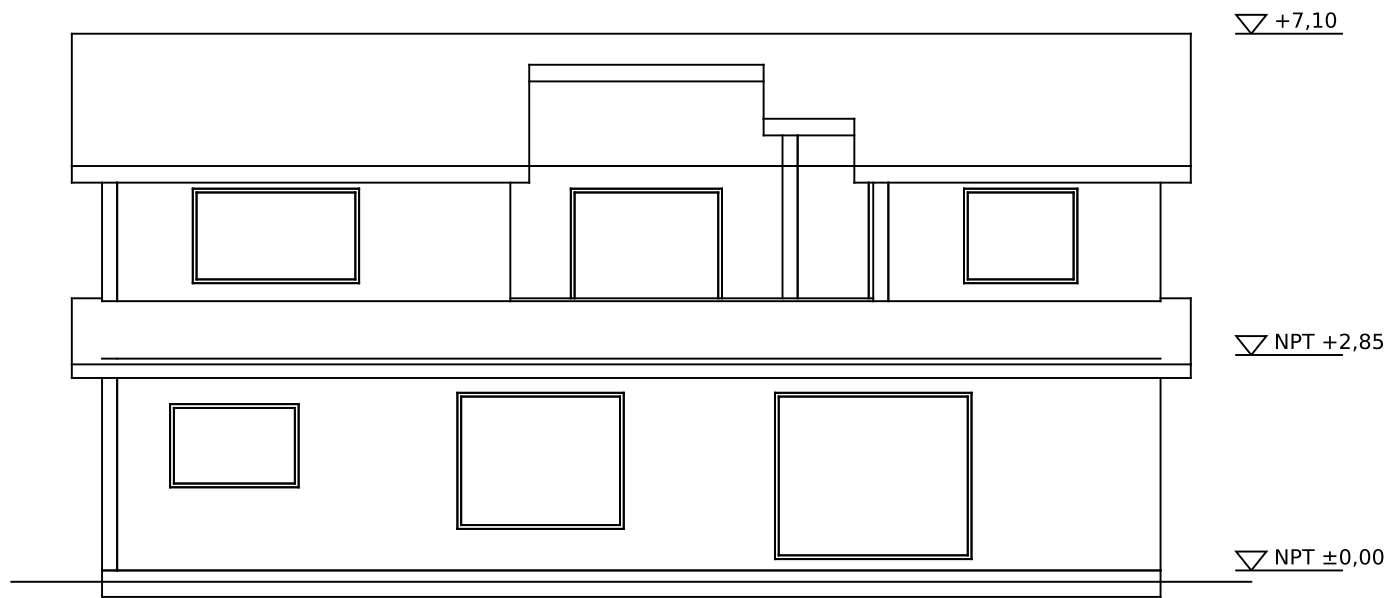

### ELEVACIÓN ORIENTE

Escala 1:100

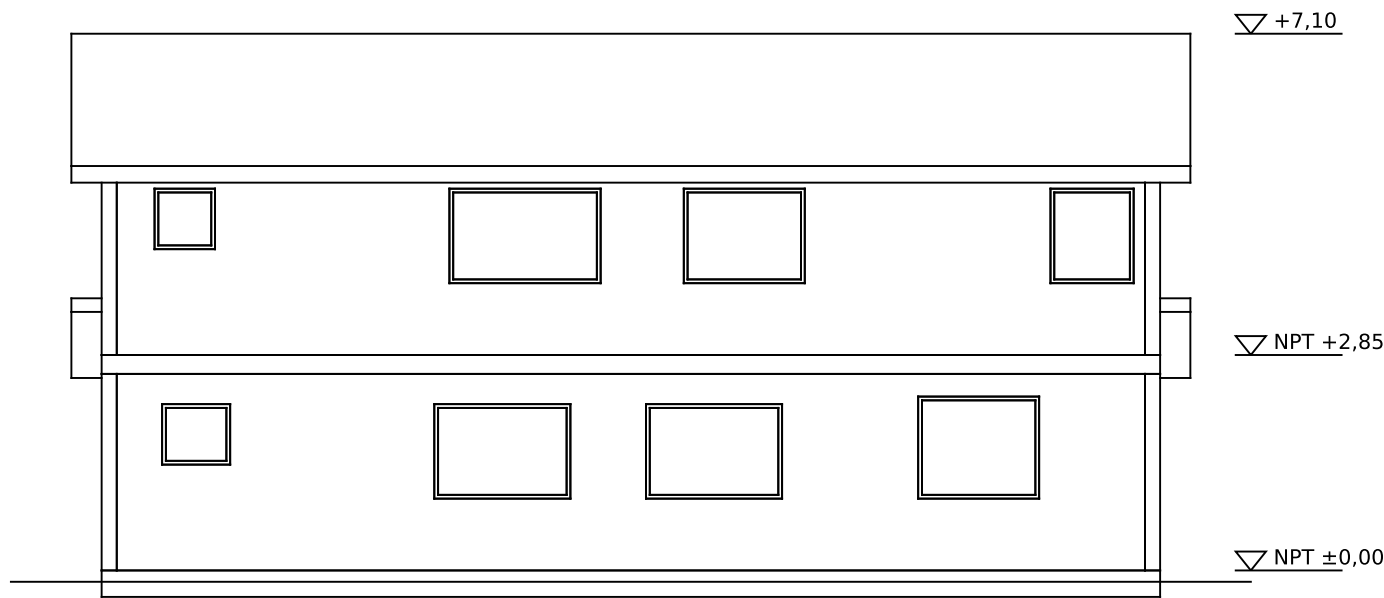

### ELEVACIÓN PONIENTE

Escala 1:100

Elevaciones proyectadas del modelo FreeCAD, sin líneas ocultas.  
Terreno a -0,15 (dato del J50N); sin levantamiento del sitio.  
Terminaciones y materiales: no están en el modelo (ver EETT).  
Cotas y niveles en metros. NPT ±0,00.  
Sin veredicto normativo: umbrales OGUC sin transcribir (INCONCLUSO).  
Norte según el documento rev. G; no hay levantamiento del sitio.

#### ELEVACIONES

Vivienda unifamiliar 2 pisos con patio interior — anteproyecto, versión v4

Propietario: por definir

Arquitecto: por definir Registro: por definir

Dirección: por definir

Rol: por definir · Comuna: por definir


Escala 1:100

Papel A2 (594 x 420 mm)

Fecha 2026-10-04 Rev. v4-A

LÁMINA


4 / 5

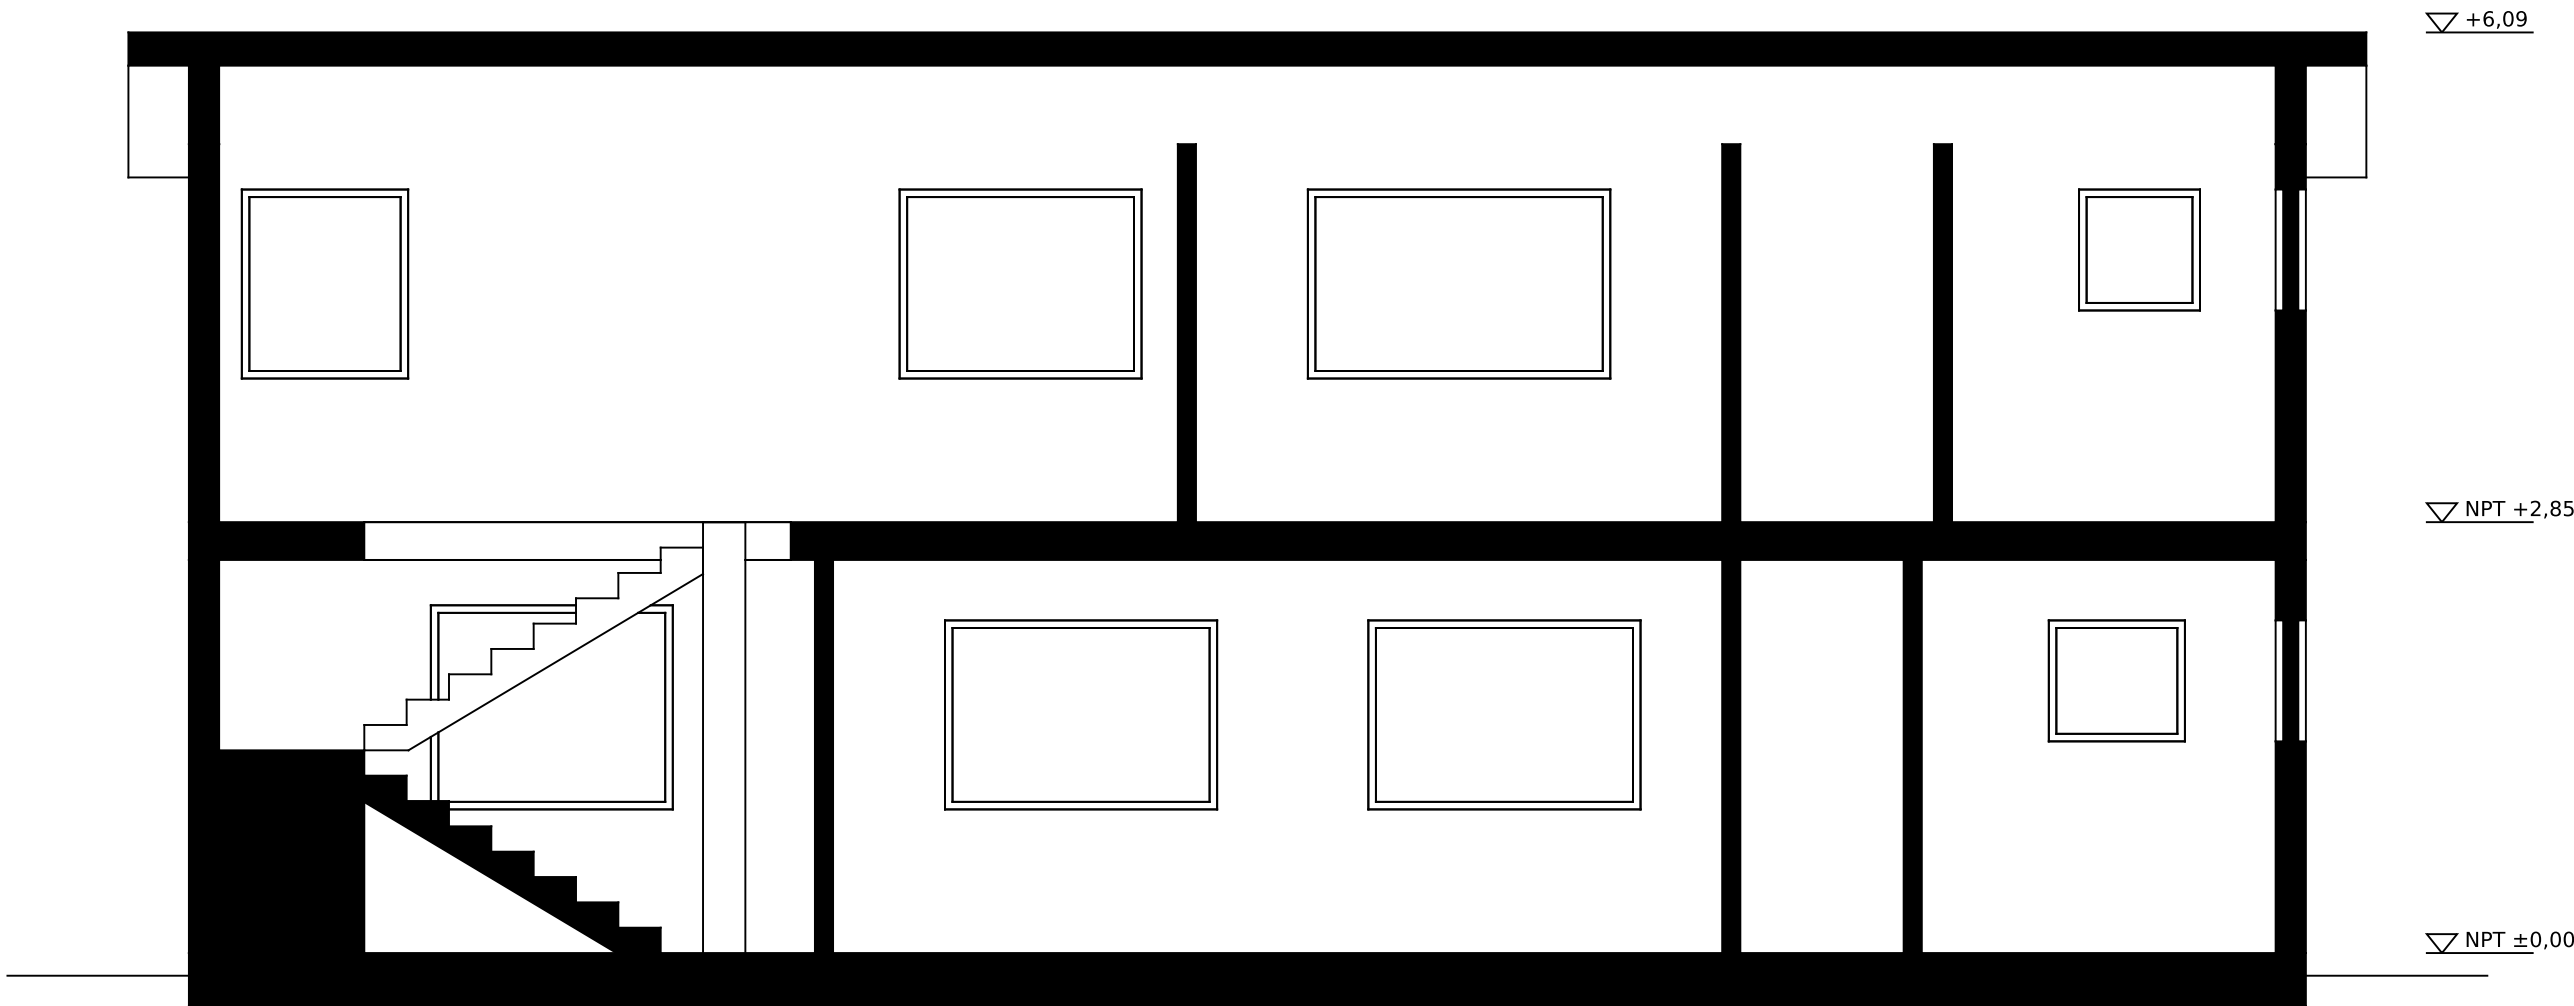

### CORTE A-A

Escala 1:50

Plano X = 1,67 m, mirando al poniente

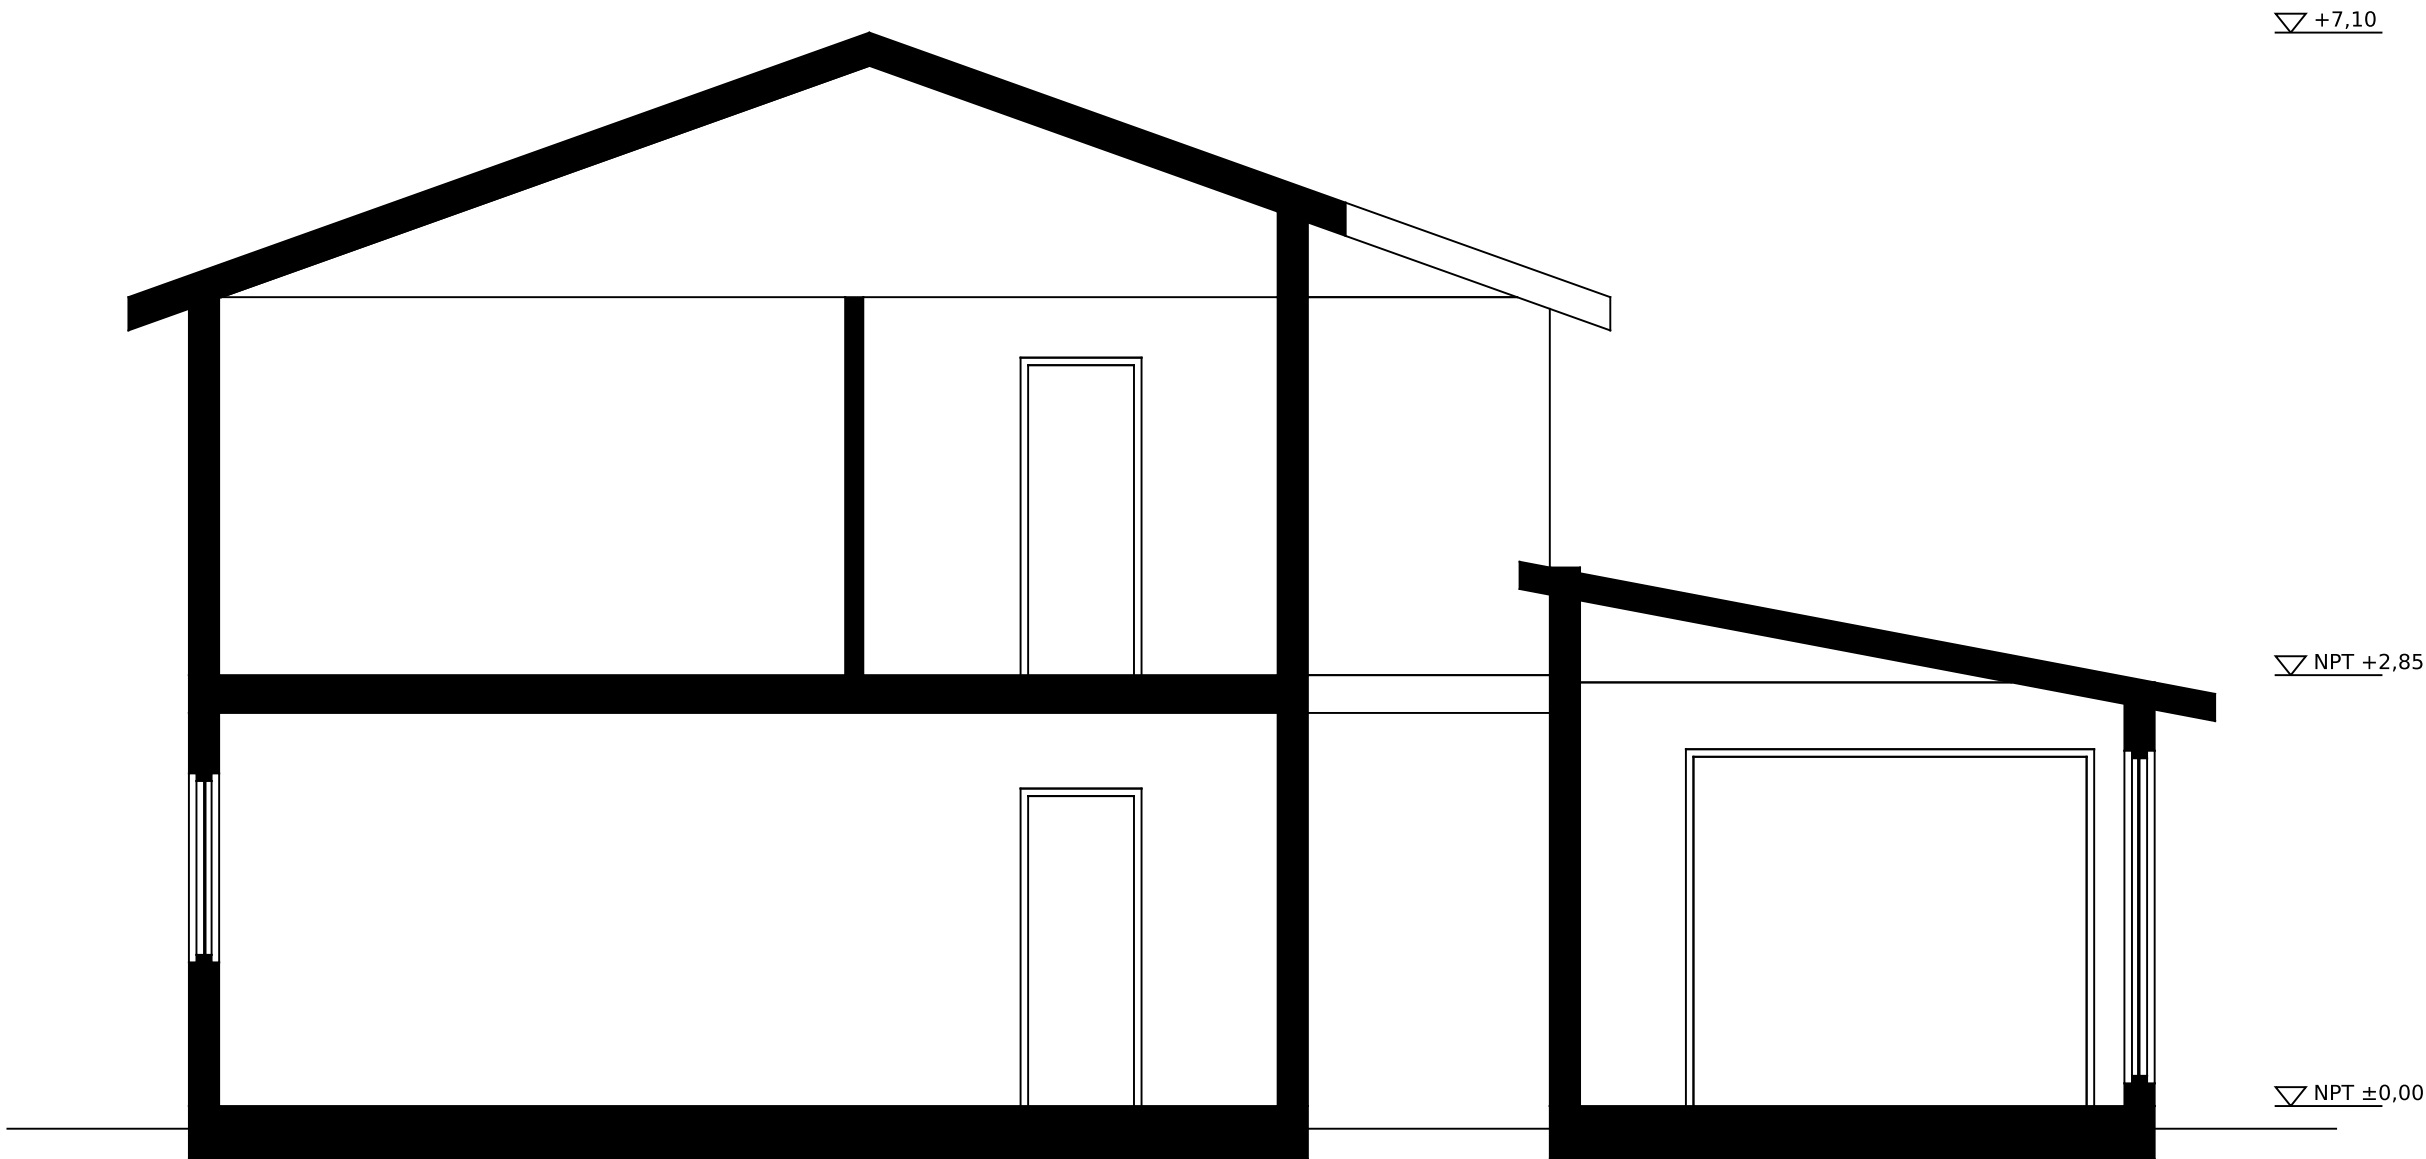

### CORTE B-B

Escala 1:50

Plano Y = -4,50 m, mirando al norte

Cortes del modelo FreeCAD; en gris, lo que corta el plano (poché).  
Ubicación de A-A y B-B: líneas de corte en las plantas.  
Holgura de escalera 1,259 m: hallazgo abierto (README de v2).  
Cotas y niveles en metros. NPT ±0,00.  
Sin veredicto normativo: umbrales OGUC sin transcribir (INCONCLUSO).  
Norte según el documento rev. G; no hay levantamiento del sitio.

### CORTES A-A Y B-B

Vivienda unifamiliar 2 pisos con patio interior — anteproyecto, versión v4

Propietario: por definir

Arquitecto: por definir Registro: por definir

Dirección: por definir

Rol: por definir · Comuna: por definir

Escala 1:50

Papel A2 (594 x 420 mm)

Fecha 2026-10-04 Rev. v4-A

LÁMINA

5 / 5